


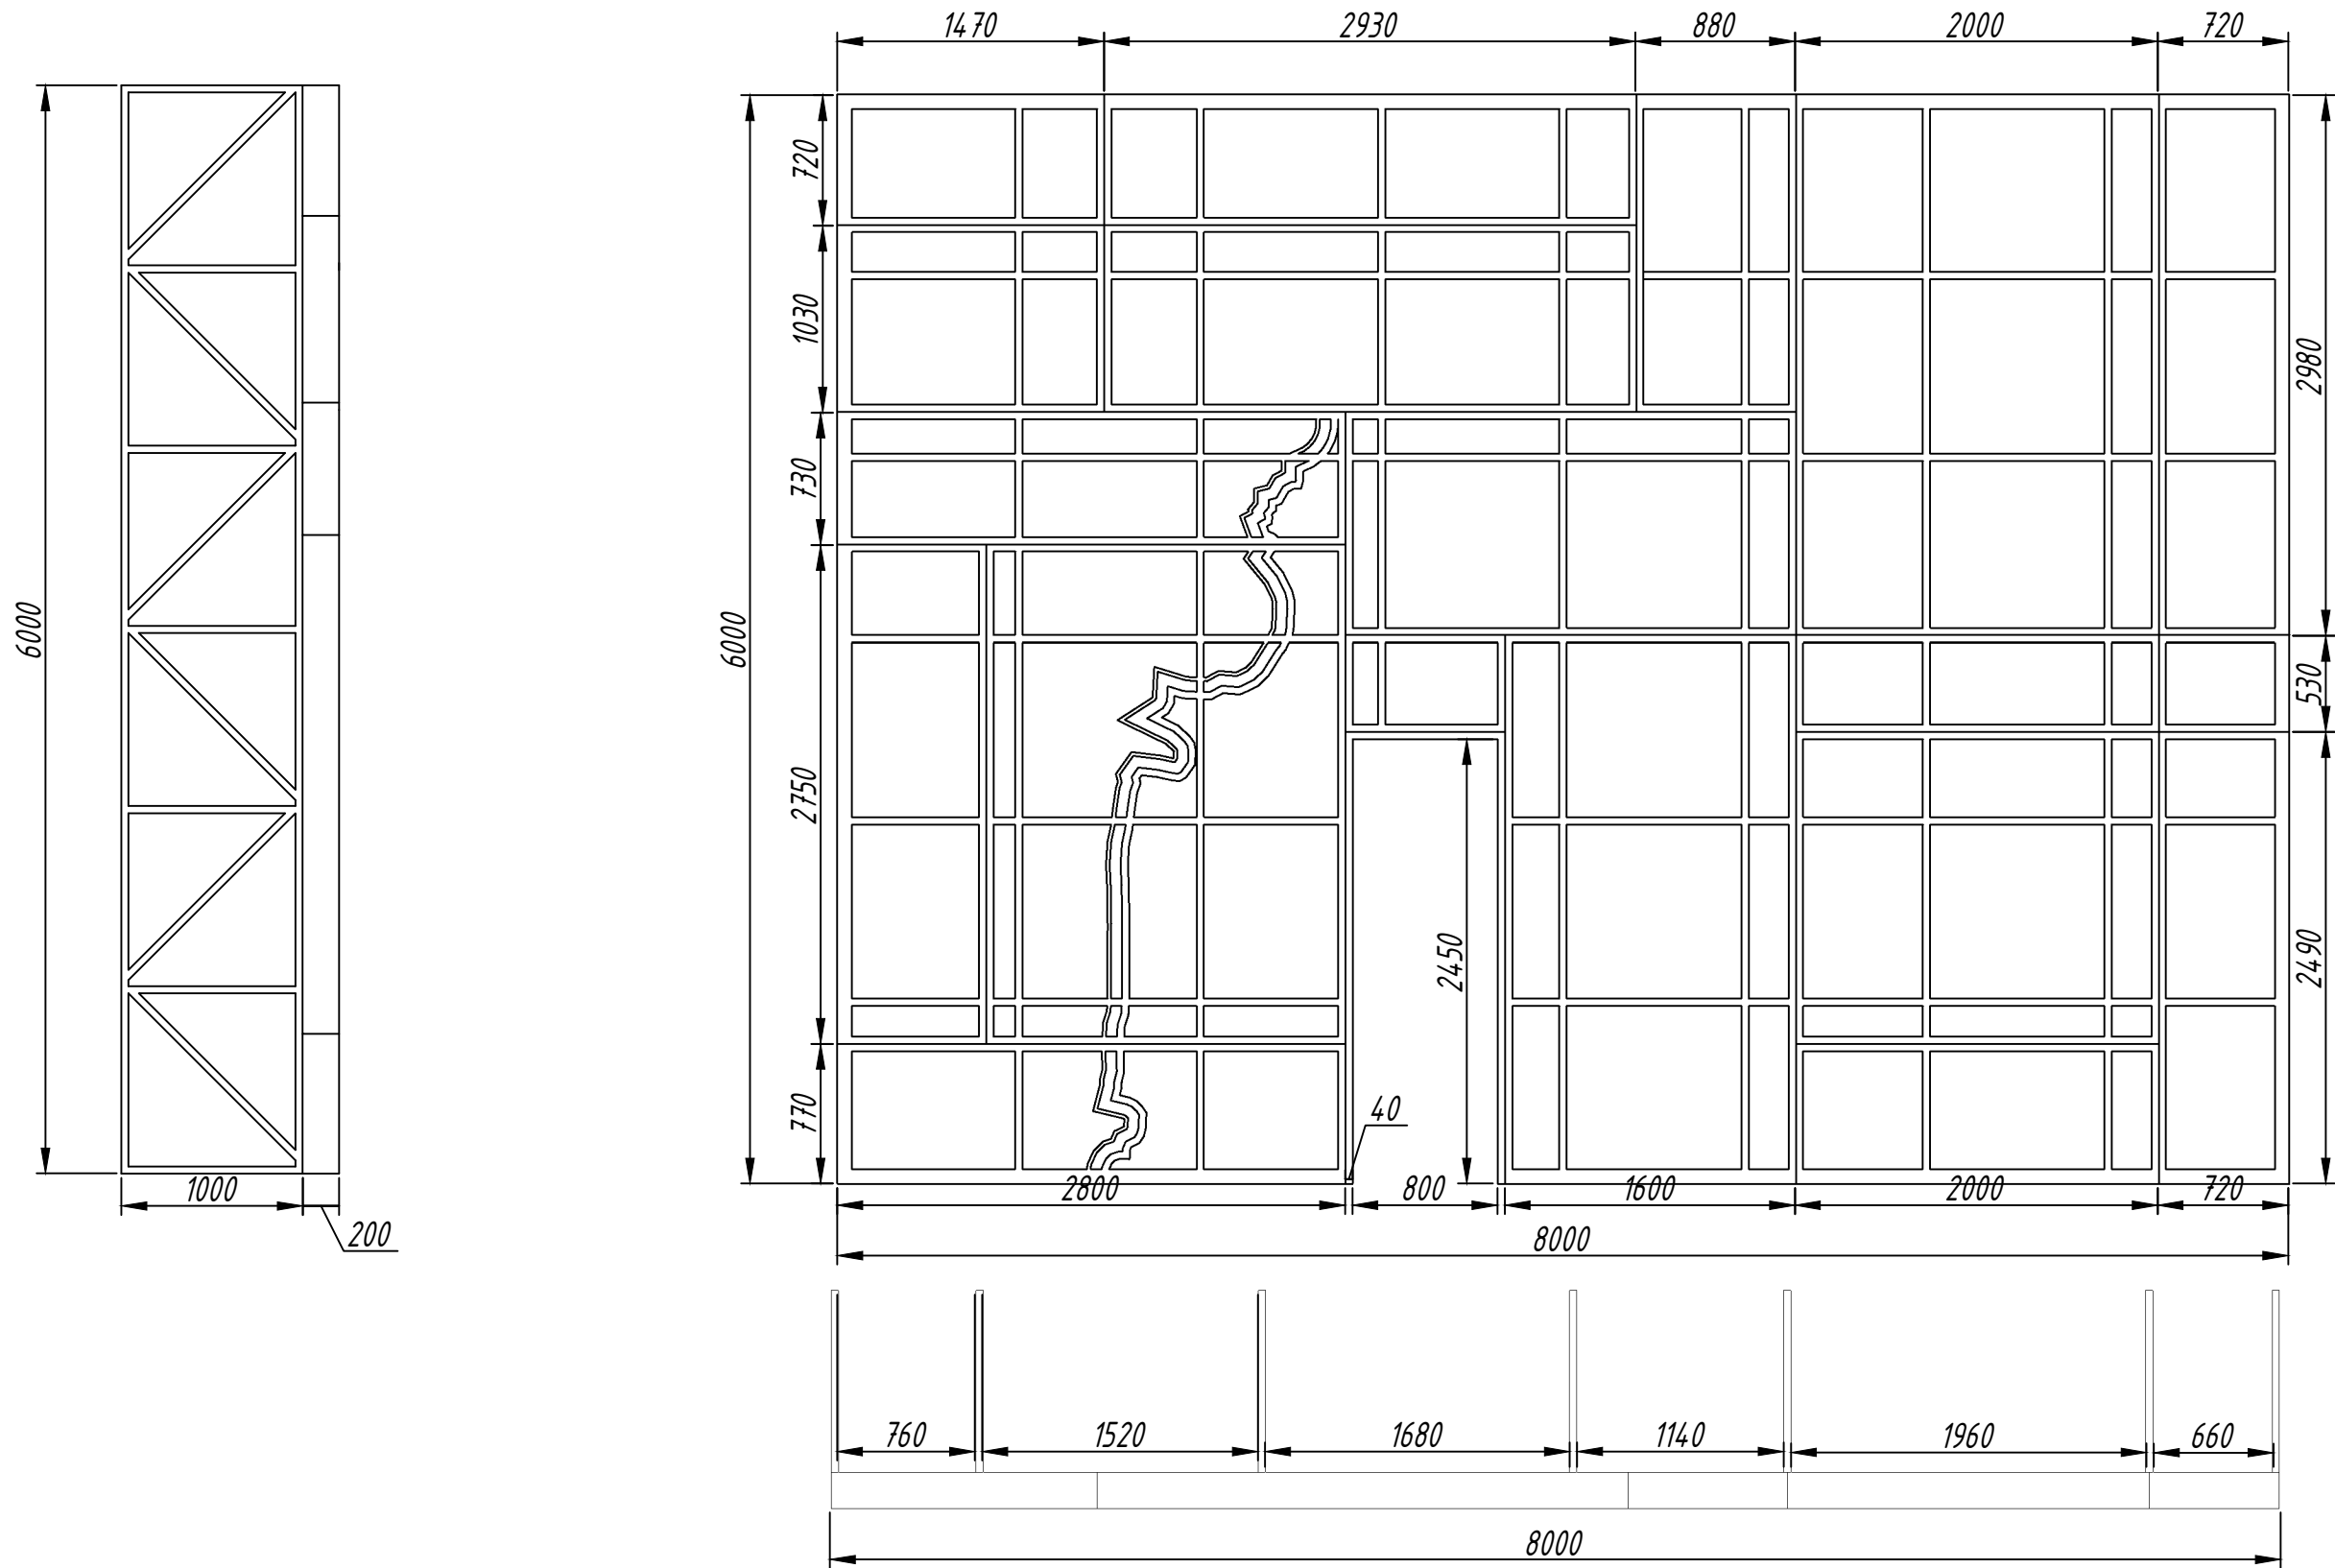

1. Выполнить каркас из алюминиевого профиля сечением 40 х 20 х 1,5 мм .
2. Выполнить конструкцию разборной .
3. Выполнить обшивку каркаса с лицевой стороны светопропускаемой тканью \ материалом (по согласованию с художником) .
4. Выполнить откосы из металлического профильного проката сечением 20 х 20 х 1,5 мм .
5. Выполнить соединение элементов комплекта между собой болтами М 8 х 60 с обеспечением надежной фиксации и плотности стыков .
6. Выполнить все соединения сварным способом .
7. Предусмотреть крепление фанеры 4 мм к лицевой части по контуру каркаса саморезами с равномерным шагом , обеспечивающим надежную фиксацию и отсутствие деформаций .
8. Предусмотреть удаление всех заусенцев и острых кромок на металлических деталях после сварки .
9. Выполнить контроль геометрических размеров и соответствия конструкции чертежу с допусками не более 1 мм .
10. Предусмотреть качество поверхности металла без дефектов , трещин , вмятин и коррозии .
11. Выполнить защитное покрытие металлоконструкции согласно техническим требованиям (при необходимости) .
12. Предусмотреть маркировку и упаковку изделия для сохранности при транспортировке и хранении .

ТХОС 1.01.-01				"Молодожены" Богомолов К.			
	Фамилия	Подпись	Дата	Стена Центральная	Литера	Масса	Масштаб
Проверил	Галич.В.В.				У		М 1:40
						Размеры	
Принял	Галич.В.В.						
				ГБУК г.Москвы "Театр на Малой Бронной"	Лист		Листов
Чертил	Глухов И.А.				Школа - студия МХАТ		