


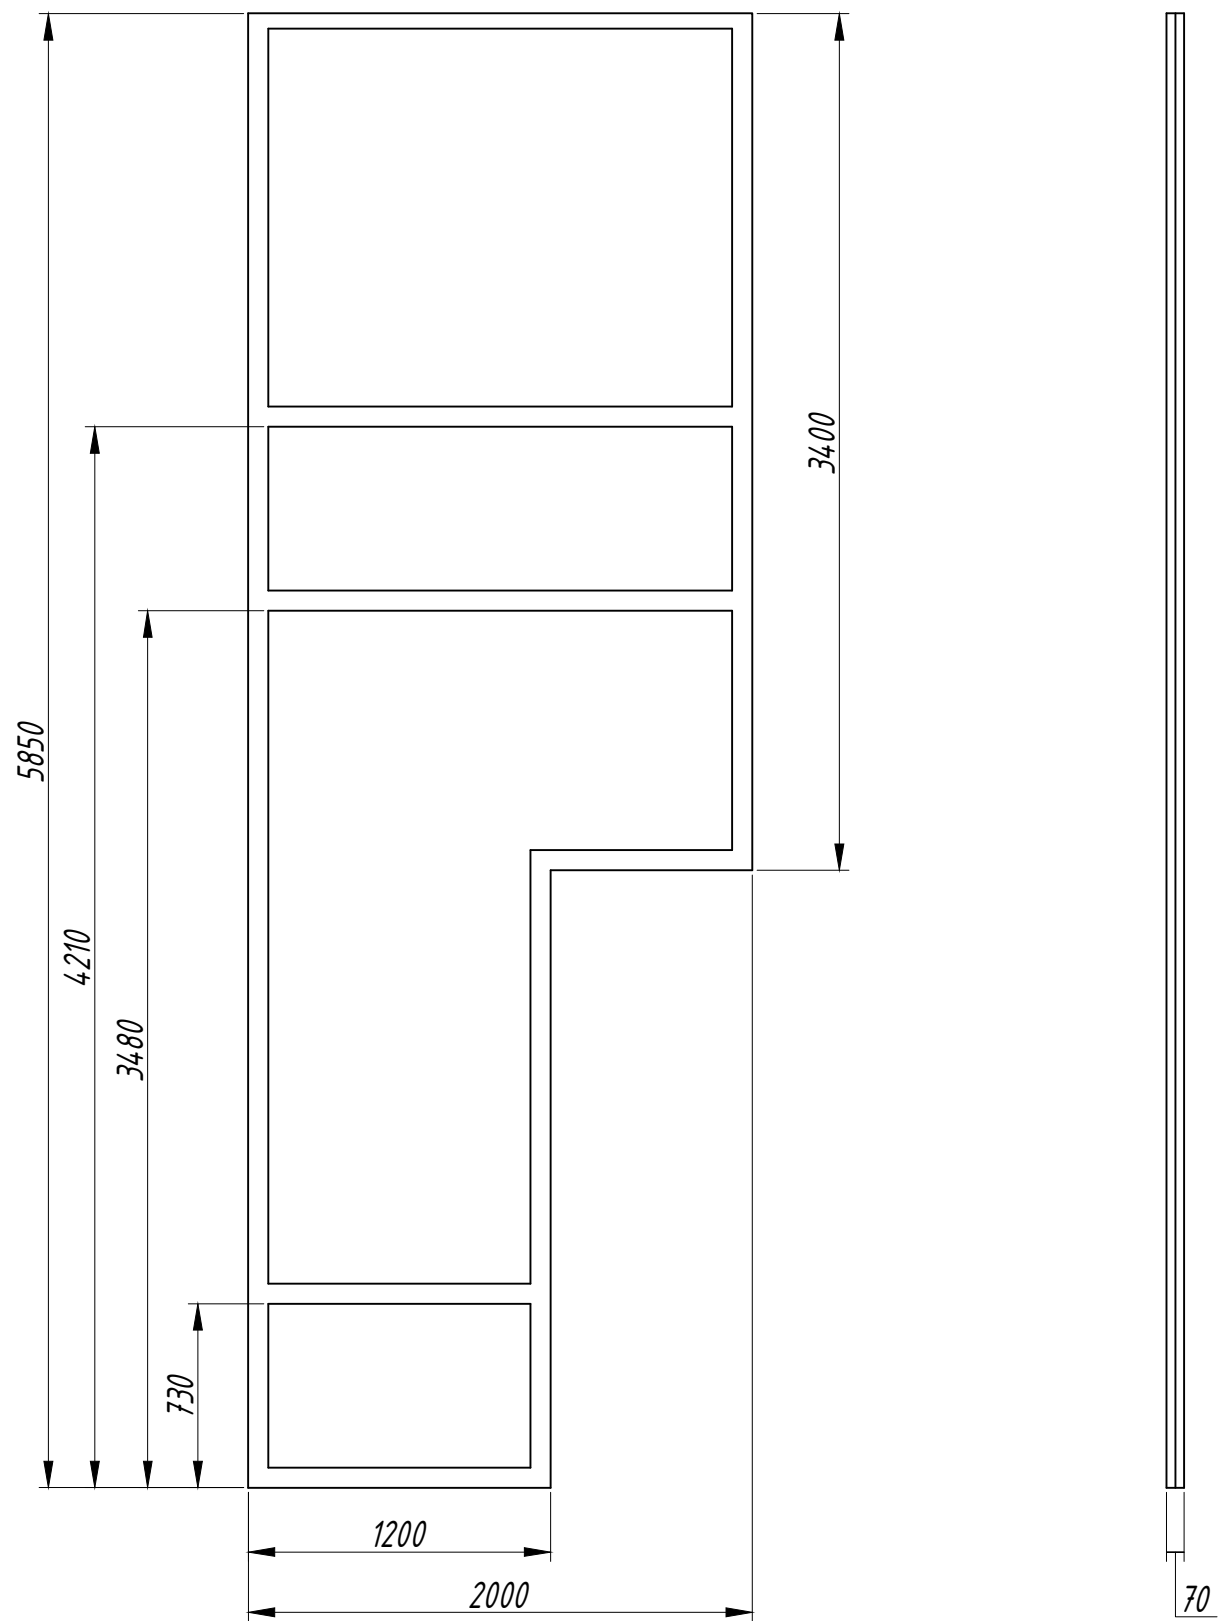

Стенка порталная левая устанавливается внутри проёма архитектурного портала сцены слева, перпендикулярно линии авансцены.

1. Плоская разборная конструкция. Делить на 2 (возможно 3) части, ближе к центру стены, стык выполнить по черной декоративной накладке.
2. Каркас – металл/алюминиевый профиль
3. Передний край стенки установить вровень с порталной стеной театра.
4. По низу стенки предусмотреть крепления саморезами к планшету сцены.
5. По верху стенки – соединение с «Потолком».
6. Чёрные полосы выполнить из тонкой фанеры (4–6 мм), внакладку по плоскости стенки; окрасить в матовый чёрный.
7. Основную плоскость стенки декорировать под фактуру гладкой штукатурки.

ТХОС 1.02.-1-9				"Молодожены" Богомолов К.			
	Фамилия	Подпись	Дата	Стена левая. Габариты.	Литера	Масса	Масштаб
Проверил	Галич.В.В.				У		М 1:30
						Размеры	
Принял	Галич.В.В.						
				ГБУК г.Москвы "Театр на Малой Бронной"	Лист		Листов
Чертил	Глухов И.А.				Школа -студия МХАТ		