



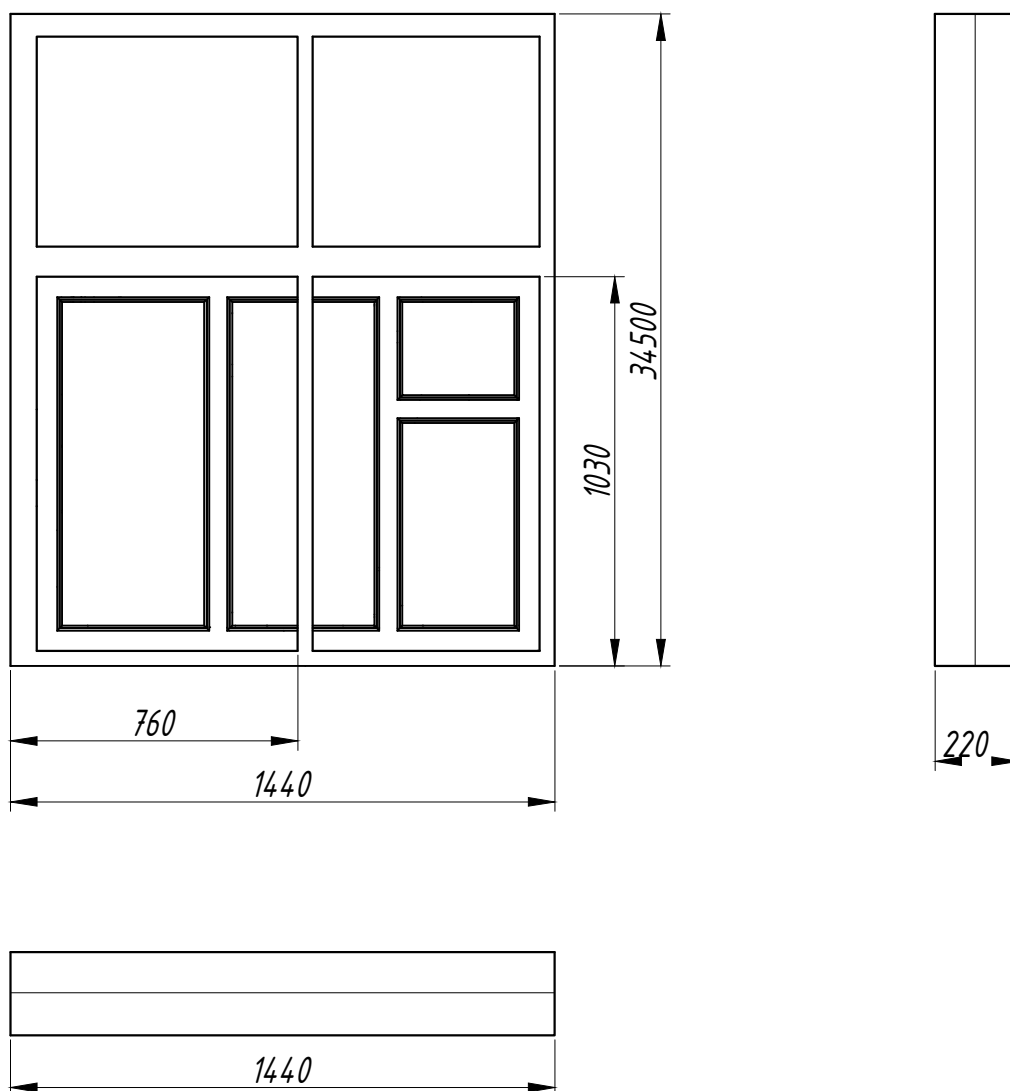


1. Является частью фронтальной стены.
2. Лайтбоксы крепятся друг к другу через болтовое соединение в единую стену.
3. Поясная сборка – от верхнего пояса к нижнему. После монтажа стена стоит на планшете сцены статично.
4. Каркас изготовить из металлопроката.
5. Облицовку натянуть translucentной баннерной тканью.
6. Чёрные полосы выполнить из тонкой фанеры (4–6 мм), внакладку по плоскости стенки, окрасить в матовый чёрный.
7. Необходимо предусмотреть быструю замену светопроницаемой ткани при её повреждении.
8. Предусмотреть места крепления светового оборудования, согласно техническому заданию художника по свету.

ТХОС 1.02.-00				"Молодожены" Богомолов К.					
	Фамилия	Подпись	Дата	Фронтальная стена. Лайтбокс 1-1.1 Габариты	Литера		Масса	Масштаб	
Проверил	Галич.В.В.				у			М 1:20	
						Размеры			
Принял	Галич.В.В.								
					Лист		Листов		
Чертил	Глухов И.А.			ГБУК г.Москвы "Театр на Малой Бронной"		Школа - студия МХАТ			

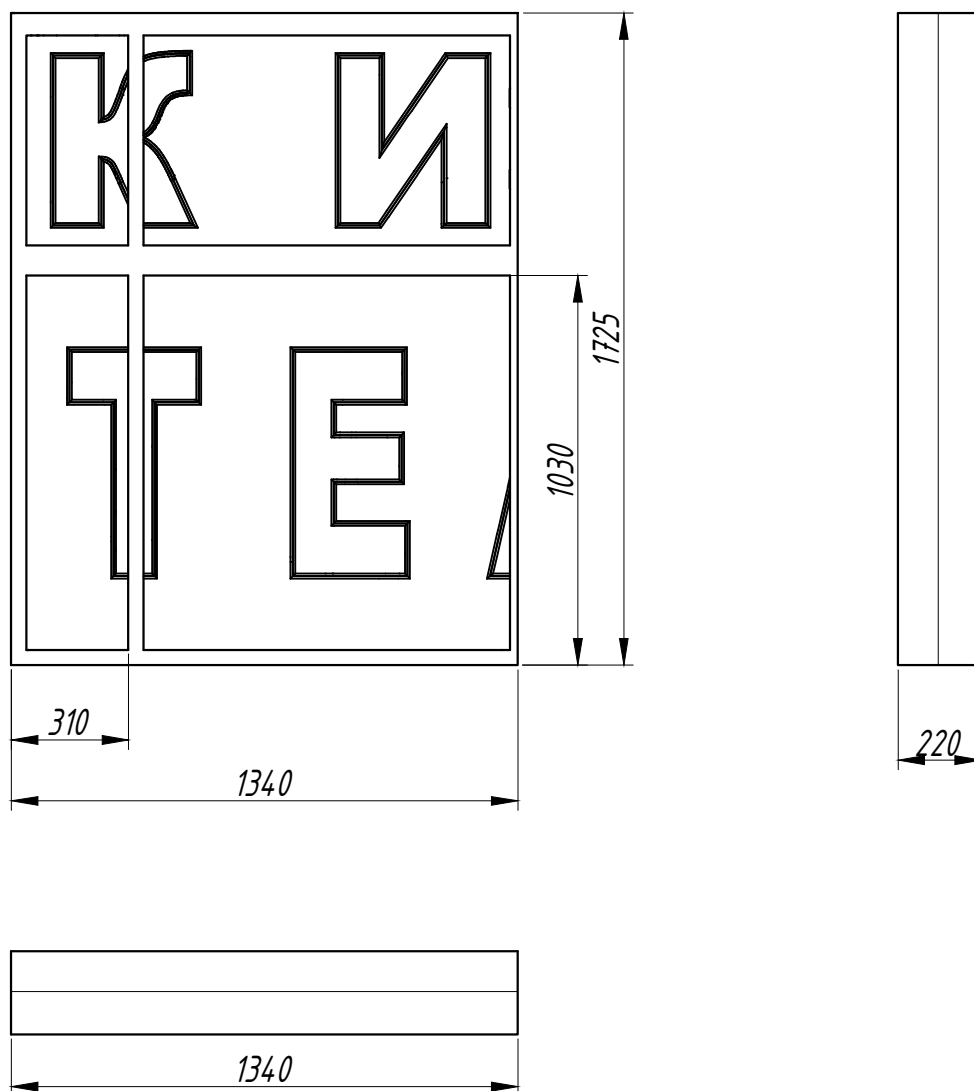



1. Является частью фронтальной стены.
2. Лайтбоксы крепятся друг к другу через болтовое соединение в единую стену.
3. Поясная сборка – от верхнего пояса к нижнему. После монтажа стена стоит на планшете сцены статично.
4. Каркас изготовить из металлопроката.
5. Облицовку натянуть translucentной баннерной тканью.
6. Чёрные полосы выполнить из тонкой фанеры (4–6 мм), внакладку по плоскости стенки, окрасить в матовый чёрный.
7. Необходимо предусмотреть быструю замену светопроницаемой ткани при её повреждении.
8. Предусмотреть места крепления светового оборудования, согласно техническому заданию художника по свету.

ТХОС 1.02.-00				"Молодожены" Богомолов К.						
	Фамилия	Подпись	Дата	Фронтальная стена. Лайтбокс 1-1.2 Габариты			Литера		Масса	Масштаб
Проверил	Галич .В .В .						у			М 1:20
Принял	Галич .В .В .									
							Лист		Листов	
Чертил	Глухов И.А.			ГБУК г.Москвы "Театр на Малой Бронной"			Школа - студия МХАТ			

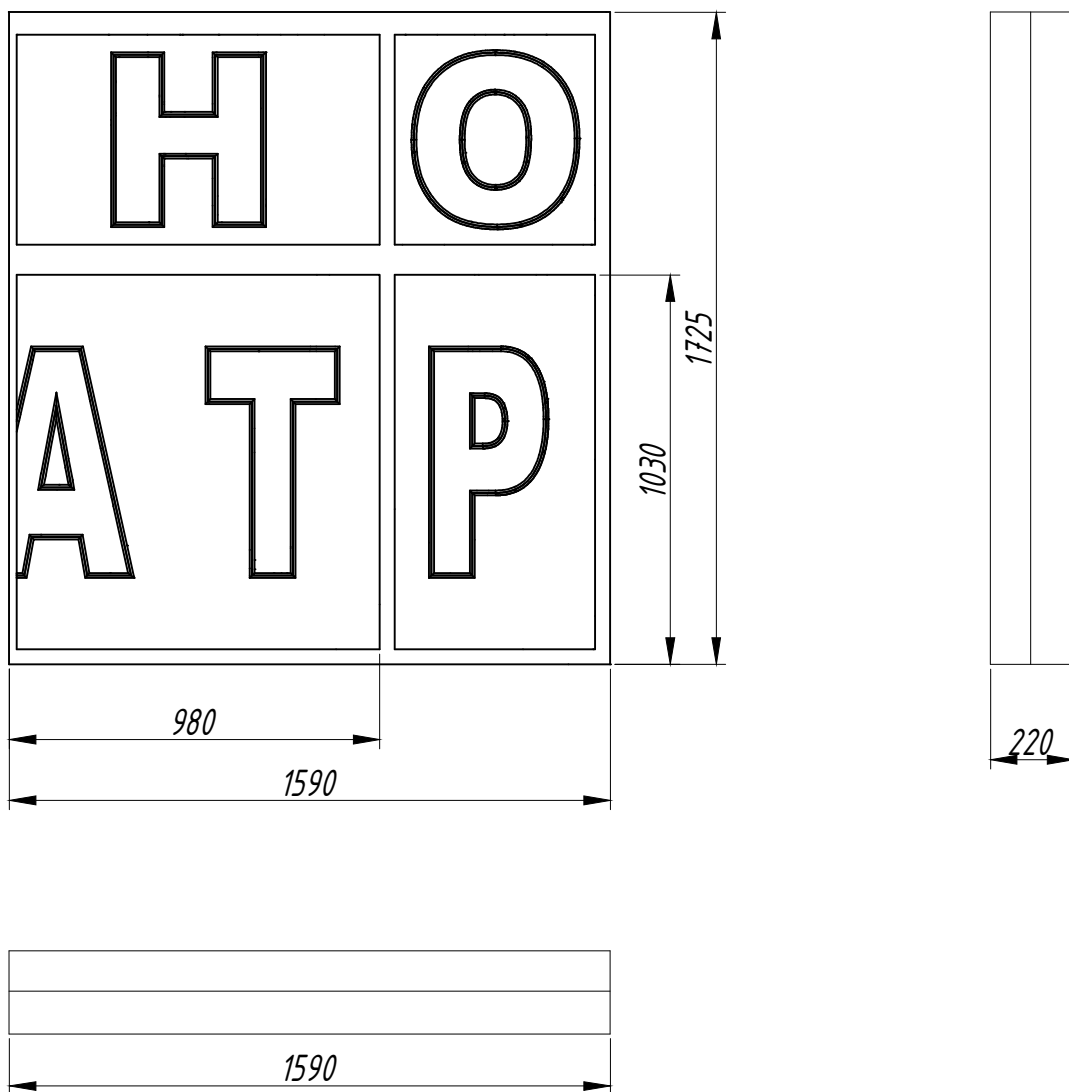


1. Является частью фронтальной стены.
2. Лайтбоксы крепятся друг к другу через болтовое соединение в единую стену.
3. Поясная сборка – от верхнего пояса к нижнему. После монтажа стена стоит на планшете сцены статично.
4. Каркас изготовить из металлопроката.
5. Облицовку натянуть translucentной баннерной тканью.
6. Чёрные полосы выполнить из тонкой фанеры (4–6 мм), внакладку по плоскости стенки, окрасить в матовый чёрный.
7. Необходимо предусмотреть быструю замену светопроницаемой ткани при её повреждении.
8. Предусмотреть места крепления светового оборудования, согласно техническому заданию художника по свету.

ТХОС 1.02.-00				"Молодожены" Богомолов К.			
	Фамилия	Подпись	Дата	Фронтальная стена. Лайтбокс 1-1.3 Габариты	Литера	Масса	Масштаб
Проверил	Галич.В.В.				у	Размеры	М 1:20
Принял	Галич.В.В.						
Чертил	Глухов И.А.				Лист	Листов	
				ГБУК г.Москвы "Театр на Малой Бронной"		Школа - студия МХАТ	

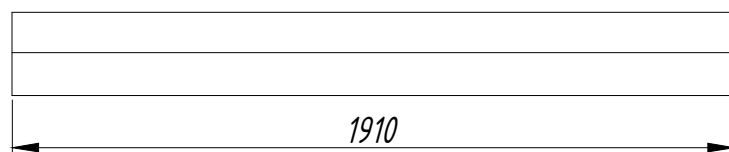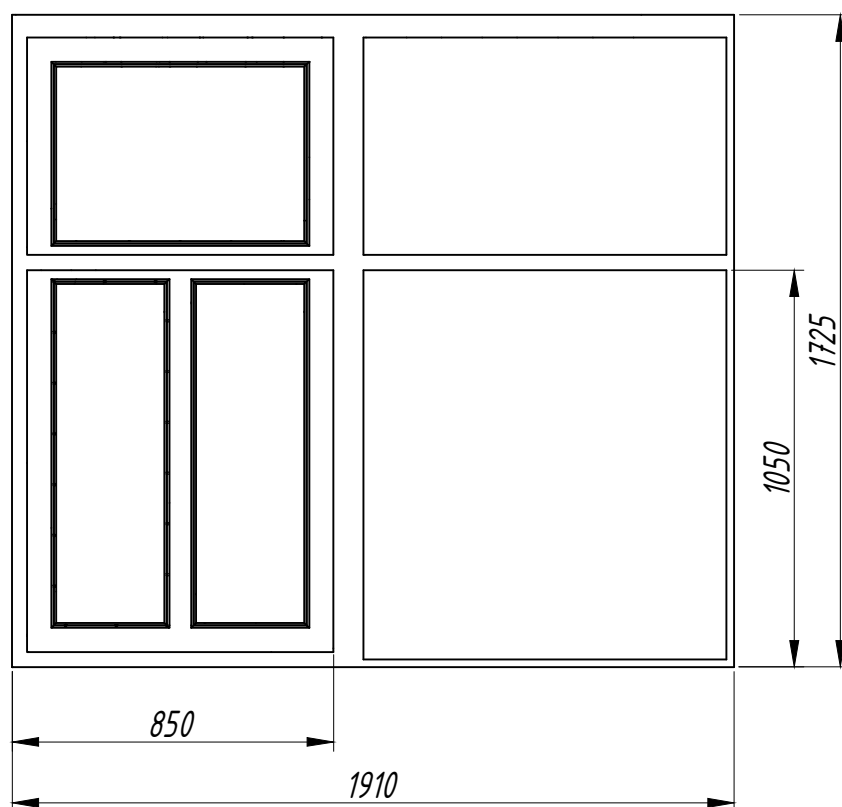


1. Является частью фронтальной стены.
2. Лайтбоксы крепятся друг к другу через болтовое соединение в единую стену.
3. Поясная сборка – от верхнего пояса к нижнему. После монтажа стена стоит на планшете сцены статично.
4. Каркас изготовить из металлопроката.
5. Облицовку натянуть translucentной баннерной тканью.
6. Чёрные полосы выполнить из тонкой фанеры (4–6 мм), внакладку по плоскости стенки, окрасить в матовый чёрный.
7. Необходимо предусмотреть быструю замену светопроницаемой ткани при её повреждении.
8. Предусмотреть места крепления светового оборудования, согласно техническому заданию художника по свету.

ТХОС 1.02.-00				"Молодожены" Богомолов К.			
	Фамилия	Подпись	Дата	Фронтальная стена. Лайтбокс 1-1.4 Габариты	Литера	Масса	Масштаб
Проверил	Галич.В.В.				у	Размеры	М 1:20
Принял	Галич.В.В.						
					Лист	Листов	
Чертил	Глухов И.А.			ГБУК г.Москвы "Театр на Малой Бронной"	Школа - студия МХАТ		

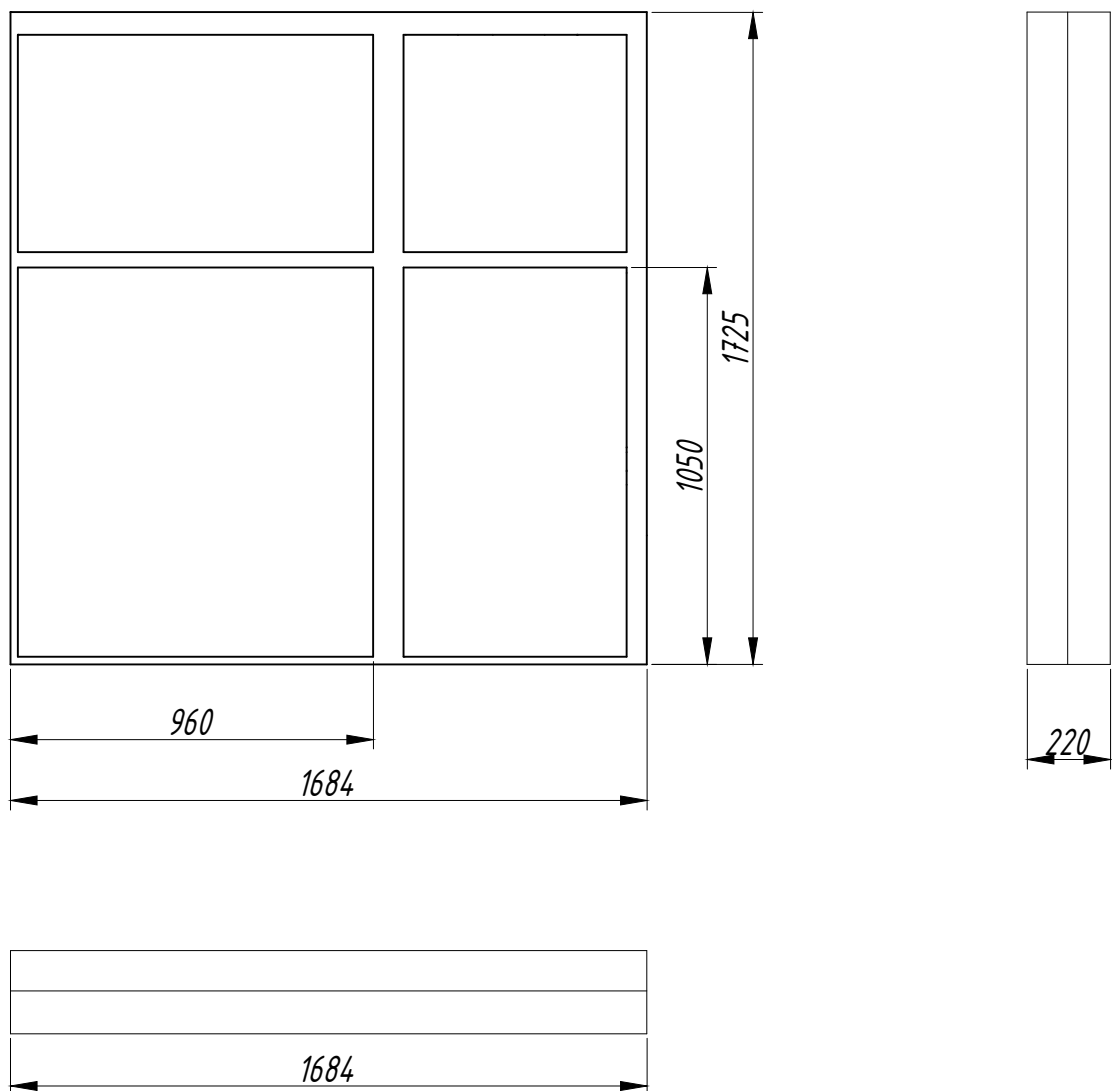


1. Является частью фронтальной стены.
2. Лайтбоксы крепятся друг к другу через болтовое соединение в единую стену.
3. Поясная сборка – от верхнего пояса к нижнему. После монтажа стена стоит на планшете сцены статично.
4. Каркас изготовить из металлопроката.
5. Облицовку натянуть translucentной баннерной тканью.
6. Чёрные полосы выполнить из тонкой фанеры (4–6 мм), внакладку по плоскости стенки, окрасить в матовый чёрный.
7. Необходимо предусмотреть быструю замену светопроницаемой ткани при её повреждении.
8. Предусмотреть места крепления светового оборудования, согласно техническому заданию художника по свету.

ТХОС 1.02.-00				"Молодожены" Богомолов К.					
	Фамилия	Подпись	Дата	Фронтальная стена. Лайтбокс 1-1.5 Габариты	Литера		Масса	Масштаб	
Проверил	Галич .В .В .				у			М 1:20	
						Размеры			
Принял	Галич .В .В .								
					Лист		Листов		
Чертил	Глухов И.А.			ГБУК г.Москвы "Театр на Малой Бронной"		Школа - студия МХАТ			

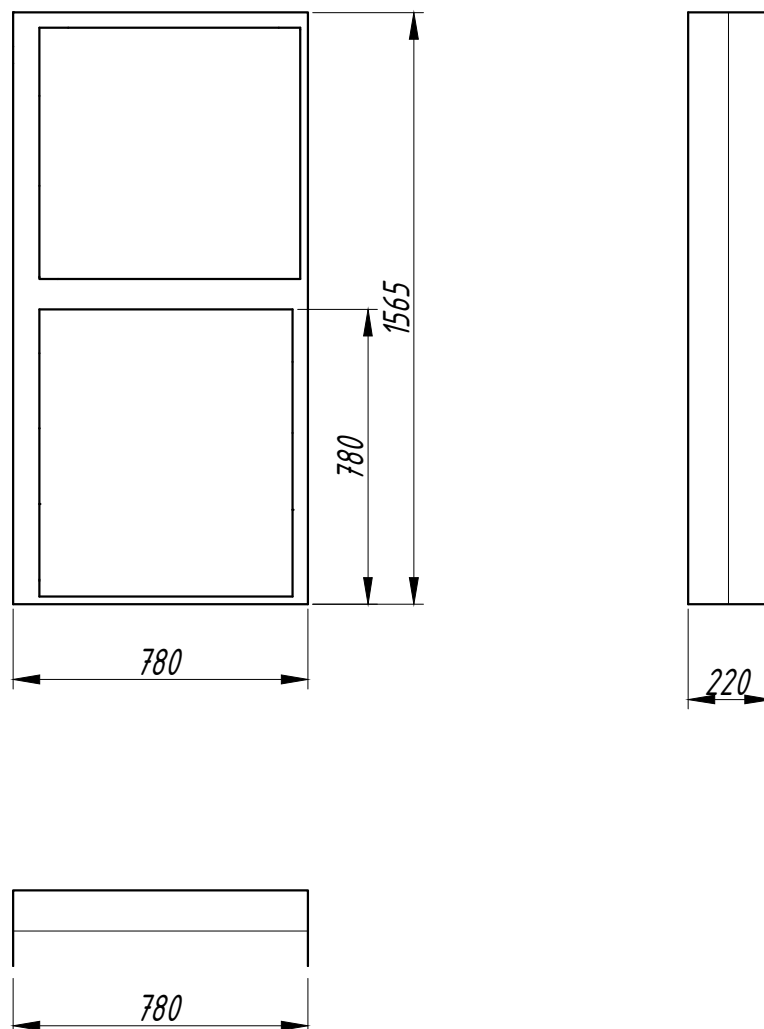


1. Является частью фронтальной стены.
2. Лайтбоксы крепятся друг к другу через болтовое соединение в единую стену.
3. Поясная сборка – от верхнего пояса к нижнему. После монтажа стена стоит на планшете сцены статично.
4. Каркас изготовить из металлопроката.
5. Облицовку натянуть translucentной баннерной тканью.
6. Чёрные полосы выполнить из тонкой фанеры (4–6 мм), внакладку по плоскости стенки, окрасить в матовый чёрный.
7. Необходимо предусмотреть быструю замену светопроницаемой ткани при её повреждении.
8. Предусмотреть места крепления светового оборудования, согласно техническому заданию художника по свету.

ТХОС 1.02.-00				"Молодожены" Богомолов К.			
	Фамилия	Подпись	Дата	Фронтальная стена. Лайтбокс 1-1.6 Габариты	Литера	Масса	Масштаб
Проверил	Галич.В.В.				у	Размеры	М 1:20
Принял	Галич.В.В.						
					Лист	Листов	
Чертил	Глухов И.А.			ГБУК г.Москвы "Театр на Малой Бронной"	Школа - студия МХАТ		

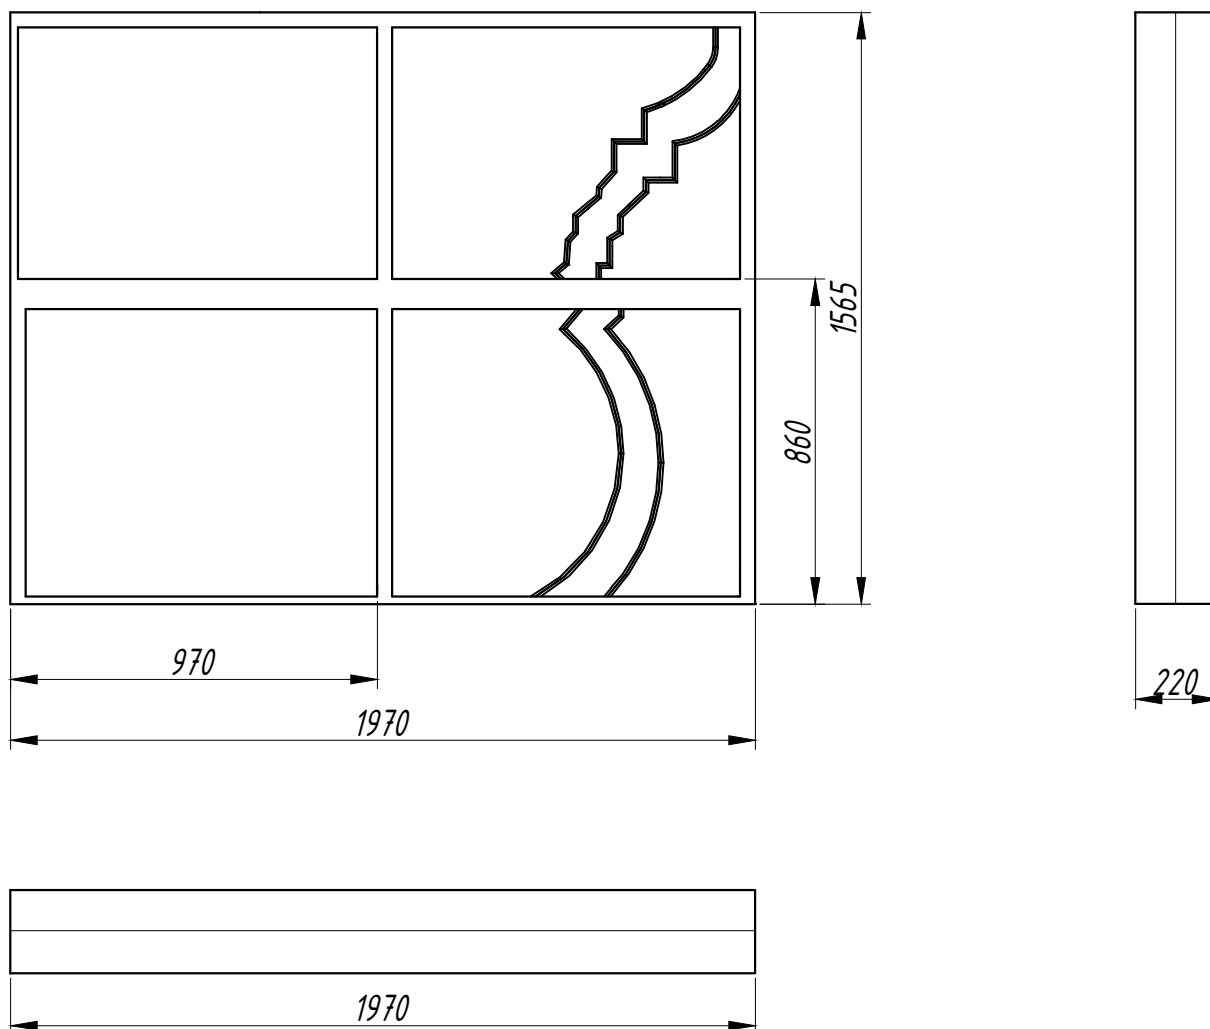


1. Является частью фронтальной стены.
2. Лайтбоксы крепятся друг к другу через болтовое соединение в единую стену.
3. Поясная сборка – от верхнего пояса к нижнему. После монтажа стена стоит на планшете сцены статично.
4. Каркас изготовить из металлопроката.
5. Облицовку натянуть translucentной баннерной тканью.
6. Чёрные полосы выполнить из тонкой фанеры (4–6 мм), внакладку по плоскости стенки, окрасить в матовый чёрный.
7. Необходимо предусмотреть быструю замену светопроницаемой ткани при её повреждении.
8. Предусмотреть места крепления светового оборудования, согласно техническому заданию художника по свету.

ТХОС 1.02.-00				"Молодожены" Богомолов К.						
	Фамилия	Подпись	Дата	Фронтальная стена. Лайтбокс 1-1.7 Габариты			Литера		Масса	Масштаб
Проверил	Галич.В.В.						у	Размеры		М 1:20
Принял	Галич.В.В.									
Чертил	Глухов И.А.			ГБУК г.Москвы "Театр на Малой Бронной"			Лист		Листов	
							Школа - студия МХАТ			

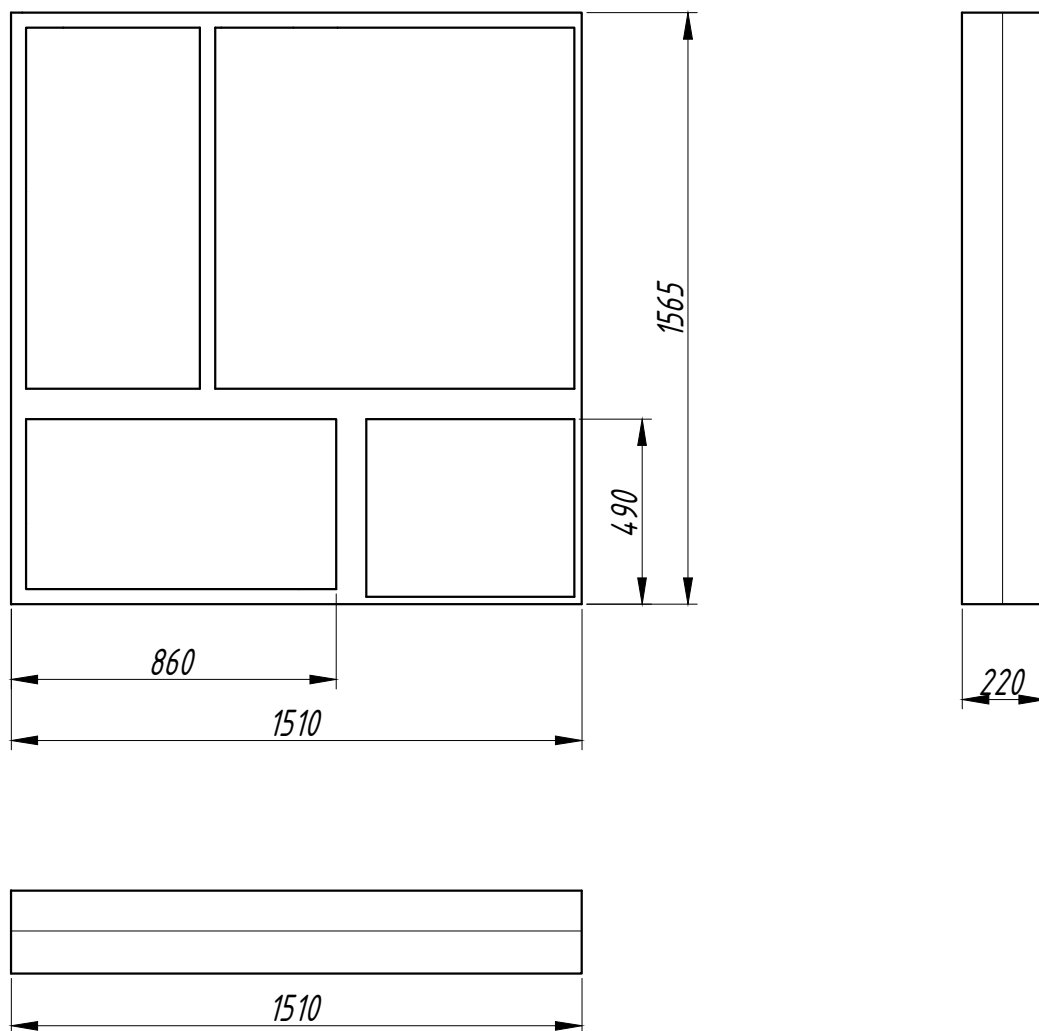


1. Является частью фронтальной стены.
2. Лайтбоксы крепятся друг к другу через болтовое соединение в единую стену.
3. Поясная сборка – от верхнего пояса к нижнему. После монтажа стена стоит на планшете сцены статично.
4. Каркас изготовить из металлопроката.
5. Облицовку натянуть translucentной баннерной тканью.
6. Чёрные полосы выполнить из тонкой фанеры (4–6 мм), внакладку по плоскости стенки, окрасить в матовый чёрный.
7. Необходимо предусмотреть быструю замену светопроницаемой ткани при её повреждении.
8. Предусмотреть места крепления светового оборудования, согласно техническому заданию художника по свету.

ТХОС 1.02.-00				"Молодожены" Богомолов К.					
	Фамилия	Подпись	Дата	Фронтальная стена. Лайтбокс 1-1.8 Габариты	Литера		Масса	Масштаб	
Проверил	Галич.В.В.				у			М 1:20	
						Размеры			
Принял	Галич.В.В.								
					Лист		Листов		
Чертил	Глухов И.А.			ГБУК г.Москвы "Театр на Малой Бронной"		Школа - студия МХАТ			

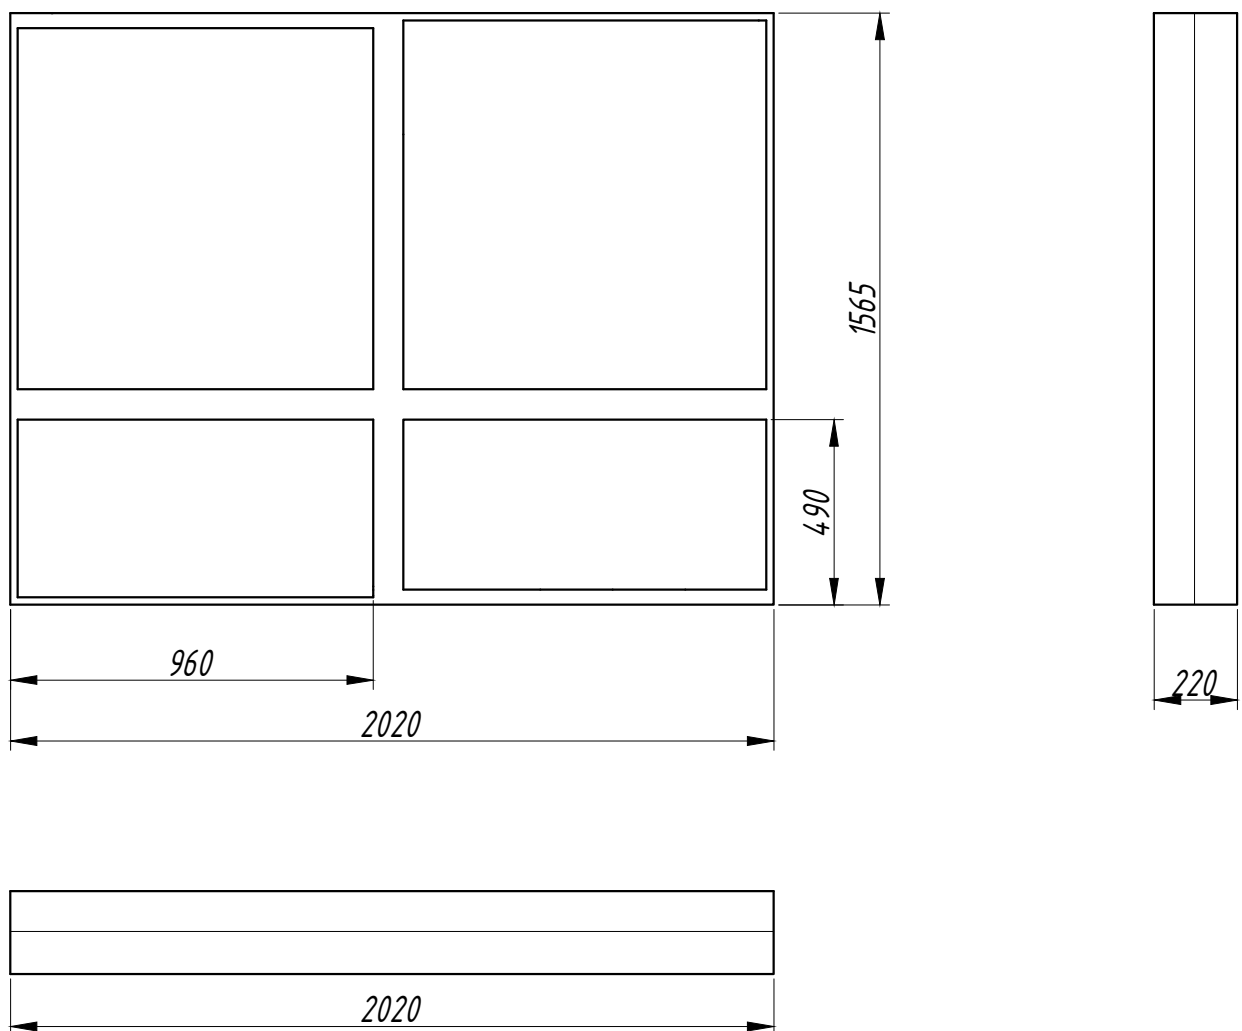


1. Является частью фронтальной стены.
2. Лайтбоксы крепятся друг к другу через болтовое соединение в единую стену.
3. Поясная сборка – от верхнего пояса к нижнему. После монтажа стена стоит на планшете сцены статично.
4. Каркас изготовить из металлопроката.
5. Облицовку натянуть translucentной баннерной тканью.
6. Чёрные полосы выполнить из тонкой фанеры (4–6 мм), внакладку по плоскости стенки, окрасить в матовый чёрный.
7. Необходимо предусмотреть быструю замену светопропускаемой ткани при её повреждении.
8. Предусмотреть места крепления светового оборудования, согласно техническому заданию художника по свету.

ТХОС 1.02.-00				"Молодожены" Богомолов К.					
	Фамилия	Подпись	Дата	Фронтальная стена. Лайтбокс 1-1.9 Габариты	Литера		Масса	Масштаб	
Проверил	Галич.В.В.				у		Размеры	М 1:20	
Принял	Галич.В.В.								
					Лист		Листов		
Чертил	Глухов И.А.			ГБУК г.Москвы "Театр на Малой Бронной"	Школа - студия МХАТ				

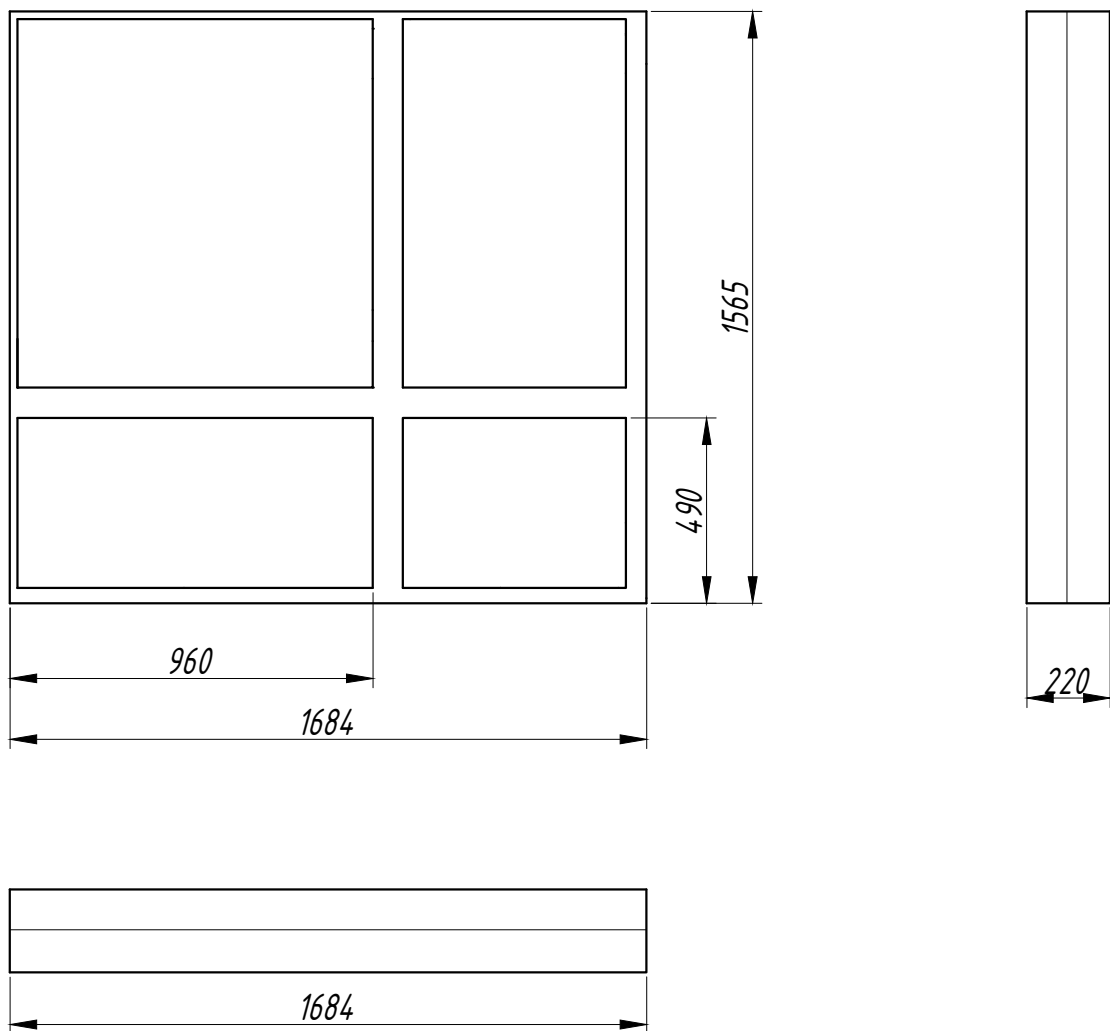


1. Является частью фронтальной стены.
2. Лайтбоксы крепятся друг к другу через болтовое соединение в единую стену.
3. Поясная сборка – от верхнего пояса к нижнему. После монтажа стена стоит на планшете сцены статично.
4. Каркас изготовить из металлопроката.
5. Облицовку натянуть translucentной баннерной тканью.
6. Чёрные полосы выполнить из тонкой фанеры (4–6 мм), внакладку по плоскости стенки, окрасить в матовый чёрный.
7. Необходимо предусмотреть быструю замену светопроницаемой ткани при её повреждении.
8. Предусмотреть места крепления светового оборудования, согласно техническому заданию художника по свету.

ТХОС 1.02.-00				"Молодожены" Богомолов К.			
	Фамилия	Подпись	Дата	Фронтальная стена. Лайтбокс 1-1.10 Габариты	Литера	Масса	Масштаб
Проверил	Галич.В.В.				у	Размеры	М 1:20
Принял	Галич.В.В.						
Чертил	Глухов И.А.				Лист	Листов	
				ГБУК г.Москвы "Театр на Малой Бронной"		Школа - студия МХАТ	

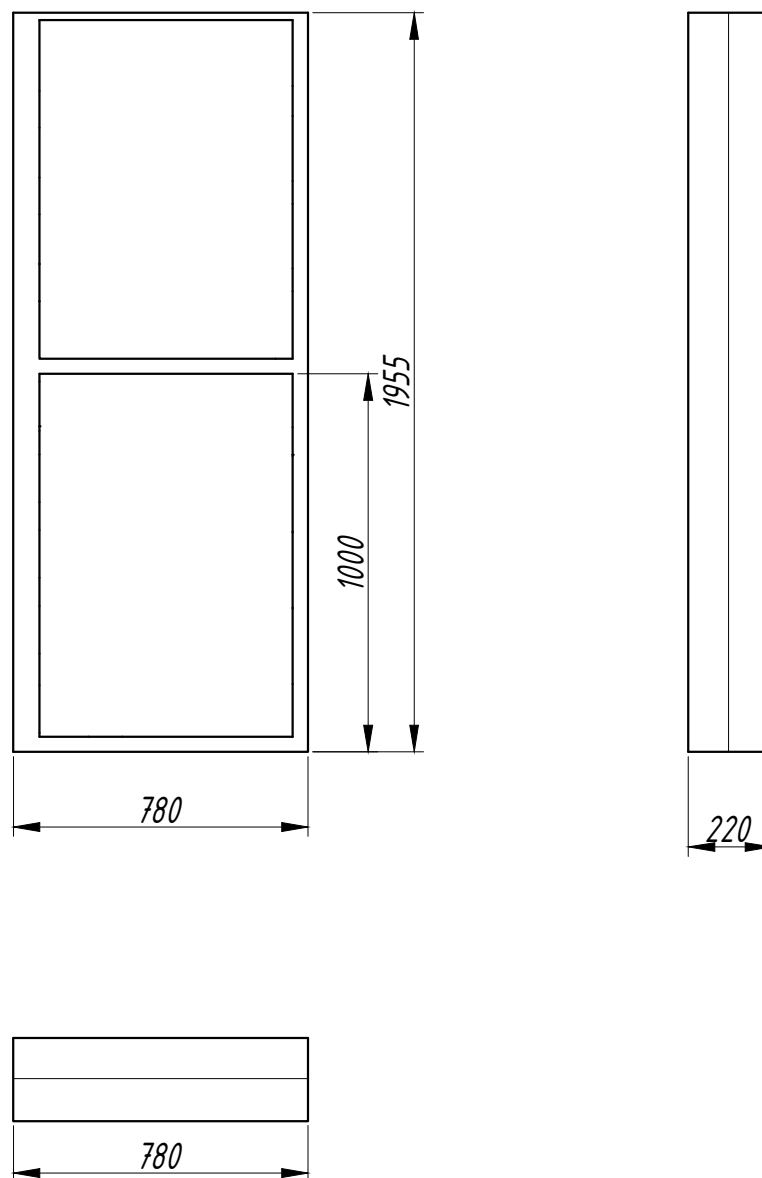


1. Является частью фронтальной стены.
2. Лайтбоксы крепятся друг к другу через болтовое соединение в единую стену.
3. Поясная сборка – от верхнего пояса к нижнему. После монтажа стена стоит на планшете сцены статично.
4. Каркас изготовить из металлопроката.
5. Облицовку натянуть translucentной баннерной тканью.
6. Чёрные полосы выполнить из тонкой фанеры (4–6 мм), внакладку по плоскости стенки, окрасить в матовый чёрный.
7. Необходимо предусмотреть быструю замену светопроницаемой ткани при её повреждении.
8. Предусмотреть места крепления светового оборудования, согласно техническому заданию художника по свету.

ТХОС 1.02.-00				"Молодожены" Богомолов К.			
	Фамилия	Подпись	Дата	Фронтальная стена. Лайтбокс 1-1.11 Габариты	Литера	Масса	Масштаб
Проверил	Галич.В.В.				у		М 1:20
						Размеры	
Принял	Галич.В.В.				Лист		Листов
Чертил	Глухов И.А.			ГБУК г.Москвы "Театр на Малой Бронной"	Школа - студия МХАТ		

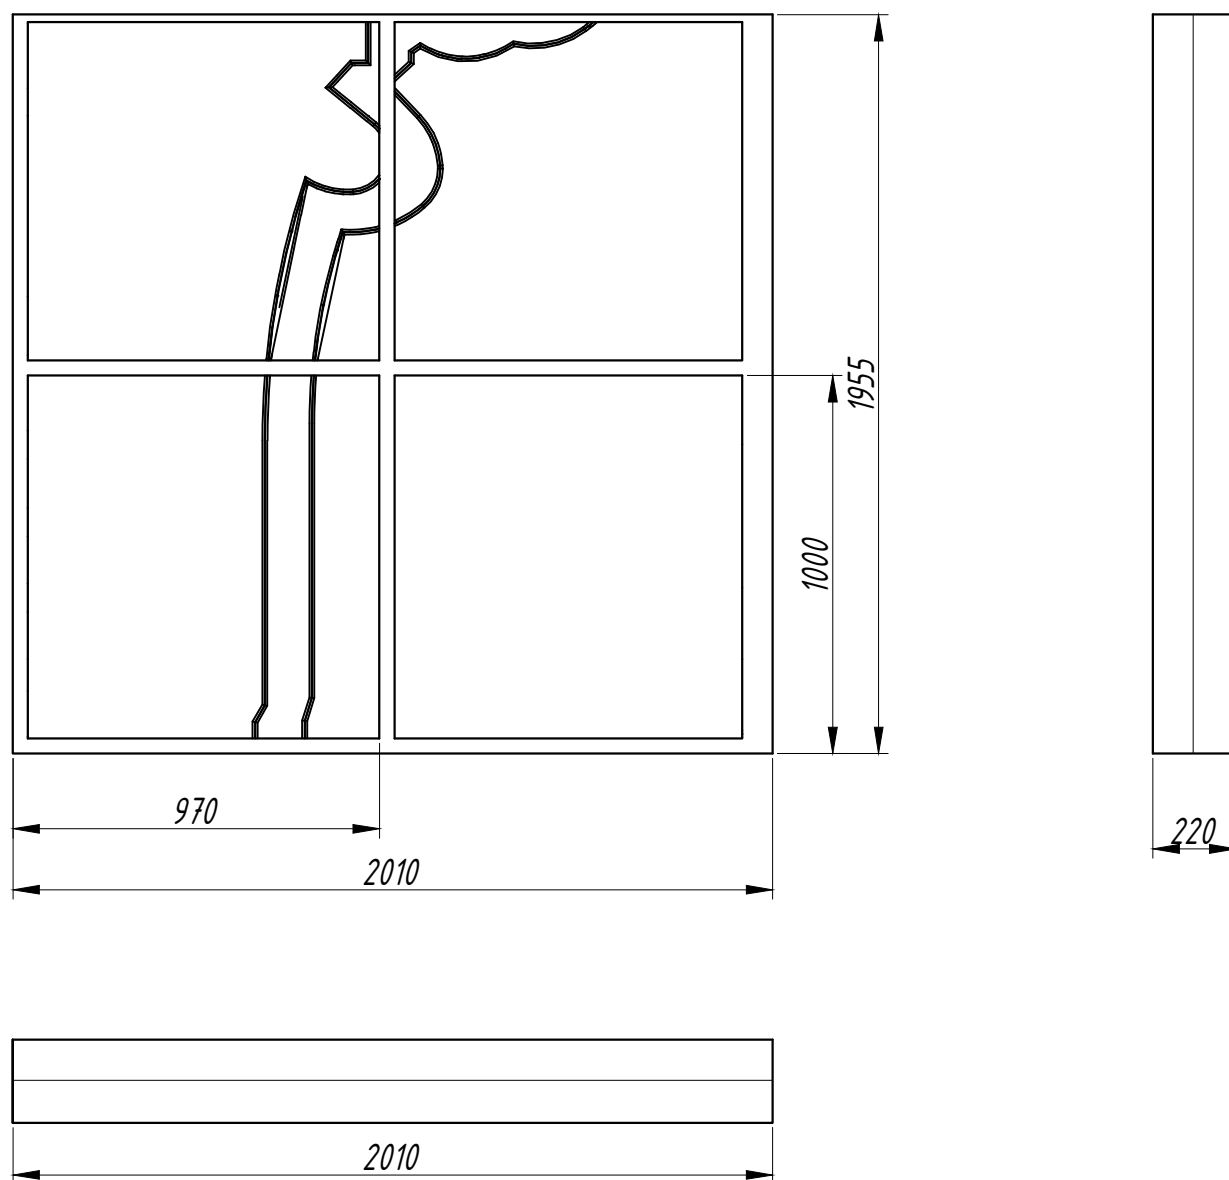


1. Является частью фронтальной стены.
2. Лайтбоксы крепятся друг к другу через болтовое соединение в единую стену.
3. Поясная сборка – от верхнего пояса к нижнему. После монтажа стена стоит на планшете сцены статично.
4. Каркас изготовить из металлопроката.
5. Облицовку натянуть translucentной баннерной тканью.
6. Чёрные полосы выполнить из тонкой фанеры (4–6 мм), внакладку по плоскости стенки, окрасить в матовый чёрный.
7. Необходимо предусмотреть быструю замену светопроницаемой ткани при её повреждении.
8. Предусмотреть места крепления светового оборудования, согласно техническому заданию художника по свету.

ТХОС 1.02.-00				"Молодожены" Богомолов К.					
	Фамилия	Подпись	Дата	Фронтальная стена. Лайтбокс 1-1.12 Габариты	Литера		Масса	Масштаб	
Проверил	Галич .В .В .				у			М 1:20	
						Размеры			
Принял	Галич .В .В .								
					Лист		Листов		
Чертил	Глухов И.А.			ГБУК г.Москвы "Театр на Малой Бронной"	Школа - студия МХАТ				

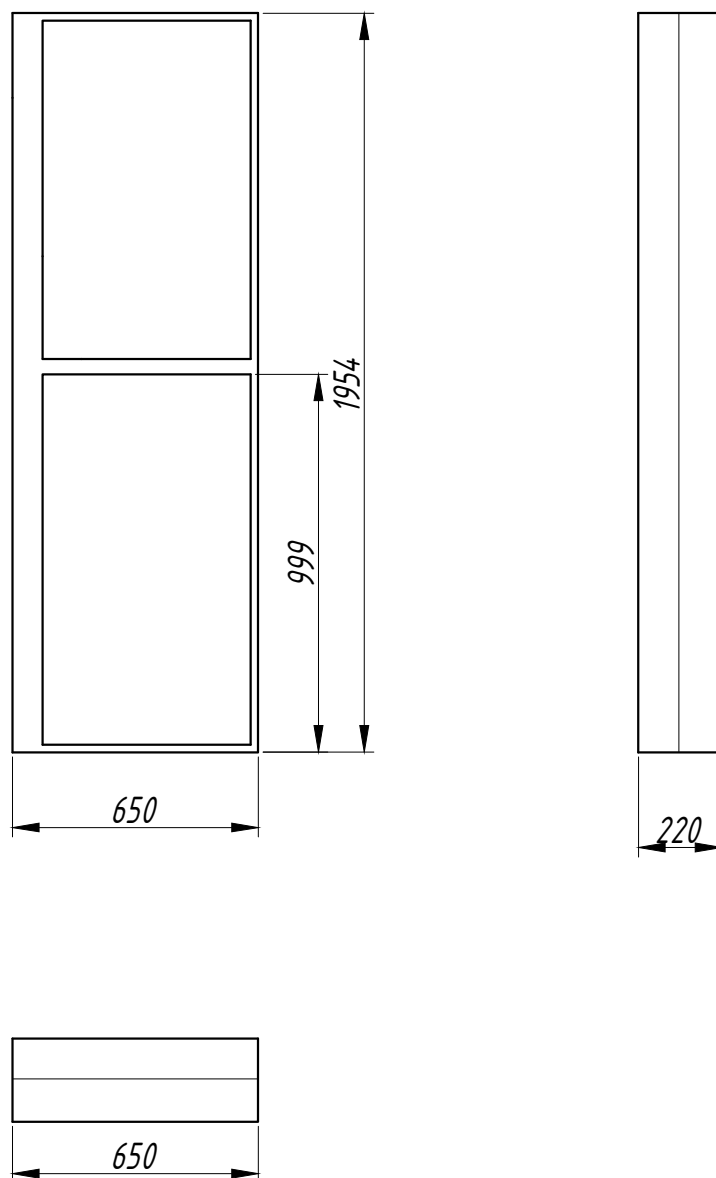


1. Является частью фронтальной стены.
2. Лайтбоксы крепятся друг к другу через болтовое соединение в единую стену.
3. Поясная сборка – от верхнего пояса к нижнему. После монтажа стена стоит на планшете сцены статично.
4. Каркас изготовить из металлопроката.
5. Облицовку натянуть translucentной баннерной тканью.
6. Чёрные полосы выполнить из тонкой фанеры (4–6 мм), внакладку по плоскости стенки, окрасить в матовый чёрный.
7. Необходимо предусмотреть быструю замену светопроницаемой ткани при её повреждении.
8. Предусмотреть места крепления светового оборудования, согласно техническому заданию художника по свету.

ТХОС 1.02.-00				"Молодожены" Богомолов К.						
	Фамилия	Подпись	Дата	Фронтальная стена. Лайтбокс 1-1.13 Габариты			Литера		Масса	Масштаб
Проверил	Галич.В.В.						у			М 1:20
									Размеры	
Принял	Галич.В.В.									
							Лист		Листов	
Чертил	Глухов И.А.			ГБУК г.Москвы "Театр на Малой Бронной"			Школа - студия МХАТ			

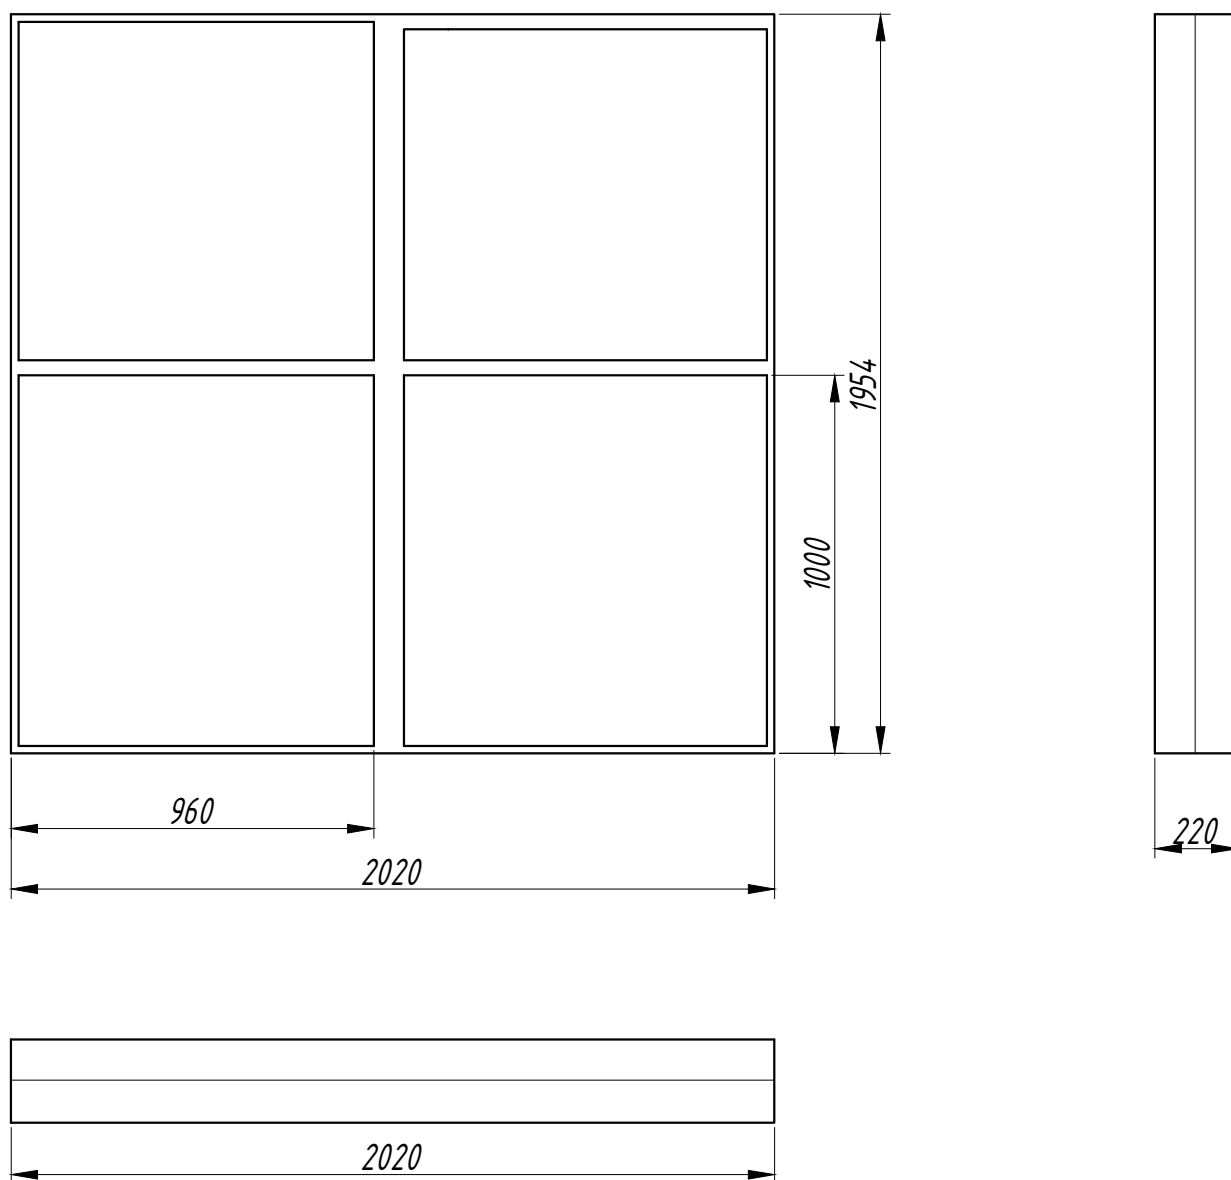




1. Является частью фронтальной стены.
2. Лайтбоксы крепятся друг к другу через болтовое соединение в единую стену.
3. Поясная сборка – от верхнего пояса к нижнему. После монтажа стена стоит на планшете сцены статично.
4. Каркас изготовить из металлопроката.
5. Облицовку натянуть translucentной баннерной тканью.
6. Чёрные полосы выполнить из тонкой фанеры (4–6 мм), внакладку по плоскости стенки, окрасить в матовый чёрный.
7. Необходимо предусмотреть быструю замену светопроницаемой ткани при её повреждении.
8. Предусмотреть места крепления светового оборудования, согласно техническому заданию художника по свету.

ТХОС 1.02.-00				"Молодожены" Богомолов К.						
	Фамилия	Подпись	Дата	Фронтальная стена. Лайтбокс 1-1.14 Габариты			Литера		Масса	Масштаб
Проверил	Галич.В.В.						у			М 1:20
									Размеры	
Принял	Галич.В.В.									
							Лист		Листов	
Чертил	Глухов И.А.			ГБУК г.Москвы "Театр на Малой Бронной"			Школа - студия МХАТ			

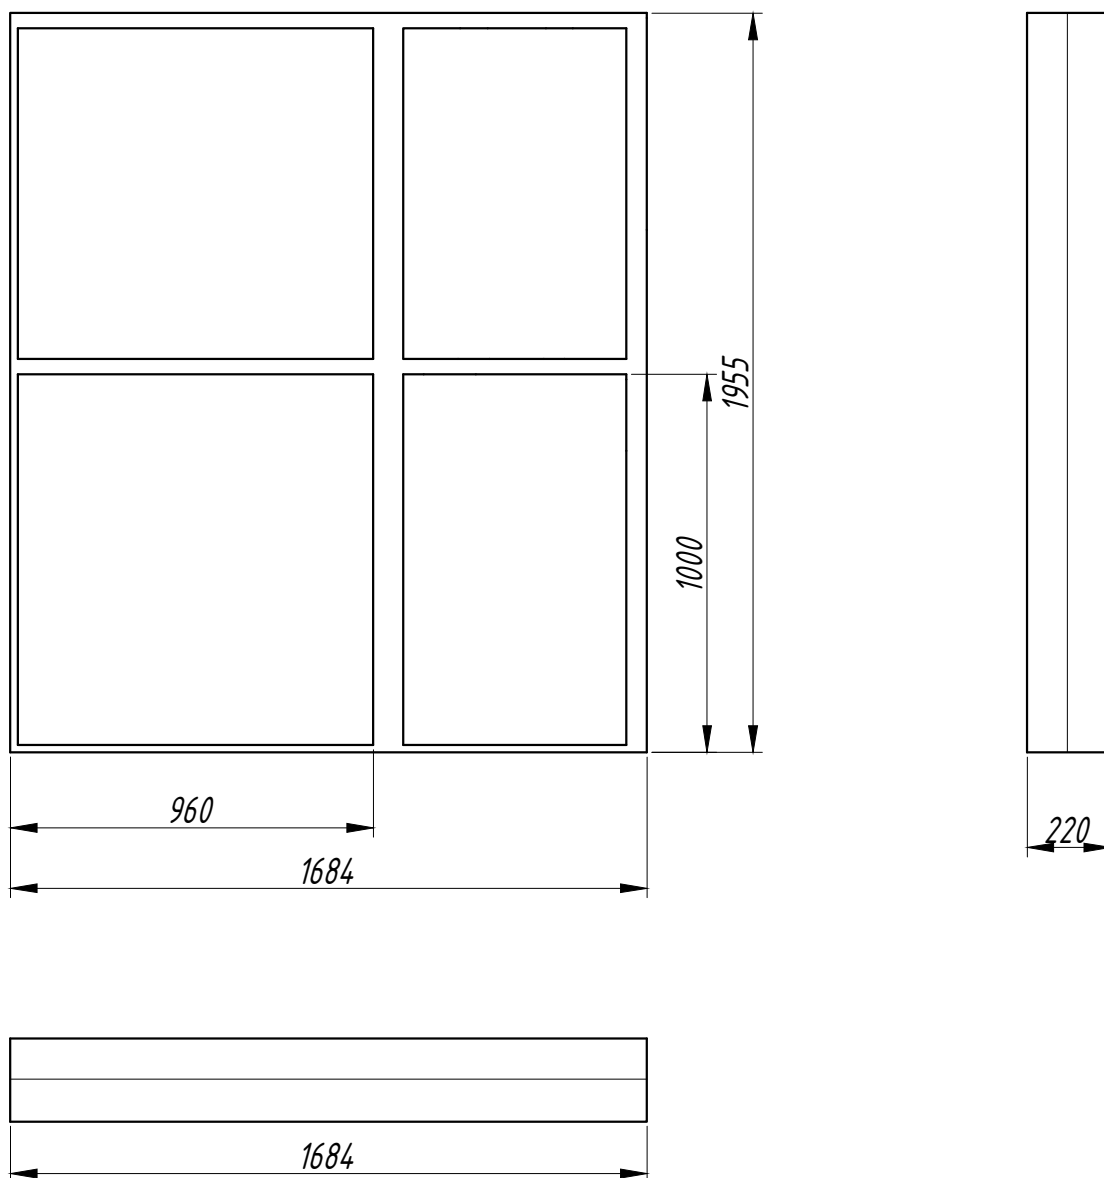




1. Является частью фронтальной стены.
2. Лайтбоксы крепятся друг к другу через болтовое соединение в единую стену.
3. Поясная сборка – от верхнего пояса к нижнему. После монтажа стена стоит на планшете сцены статично.
4. Каркас изготовить из металлопроката.
5. Облицовку затянуть translucentной баннерной тканью.
6. Чёрные полосы выполнить из тонкой фанеры (4–6 мм), внакладку по плоскости стенки, окрасить в матовый чёрный.
7. Необходимо предусмотреть быструю замену светопроницаемой ткани при её повреждении.
8. Предусмотреть места крепления светового оборудования, согласно техническому заданию художника по свету.

ТХОС 1.02.-00				"Молодожены" Богомолов К.						
	Фамилия	Подпись	Дата	Фронтальная стена. Лайтбокс 1-1.15 Габариты			Литера		Масса	Масштаб
Проверил	Галич.В.В.						у			М 1:20
									Размеры	
Принял	Галич.В.В.									
				Лист			Листов			
Чертил	Глухов И.А.			ГБУК г.Москвы "Театр на Малой Бронной"			Школа - студия МХАТ			

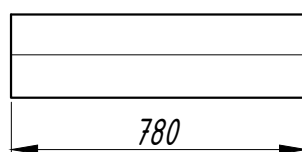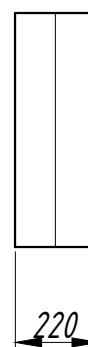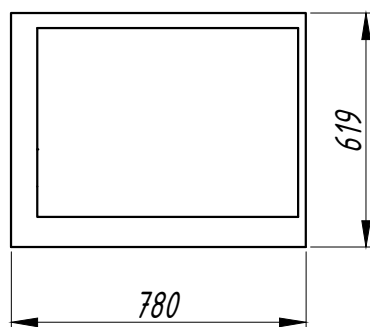




1. Является частью фронтальной стены.
2. Лайтбоксы крепятся друг к другу через болтовое соединение в единую стену.
3. Поясная сборка – от верхнего пояса к нижнему. После монтажа стена стоит на планшете сцены статично.
4. Каркас изготовить из металлопроката.
5. Облицовку затянуть транслюцентной баннерной тканью.
6. Чёрные полосы выполнить из тонкой фанеры (4–6 мм), внакладку по плоскости стенки, окрасить в матовый чёрный.
7. Необходимо предусмотреть быструю замену светопроницаемой ткани при её повреждении.
8. Предусмотреть места крепления светового оборудования, согласно техническому заданию художника по свету.

ТХОС 1.02.-00				"Молодожены" Богомолов К.							
	Фамилия	Подпись	Дата	Фронтальная стена. Лайтбокс 1-1.16 Габариты			Литера		Масса	Масштаб	
Проверил	Галич .В .В .										М 1:20
							у	Размеры			
Принял	Галич .В .В .										
Чертил	Глухов И.А.			ГБУК г.Москвы "Театр на Малой Бронной"			Лист		Листов		
							Школа - студия МХАТ				

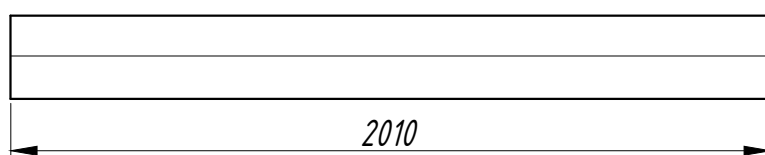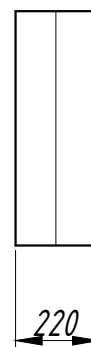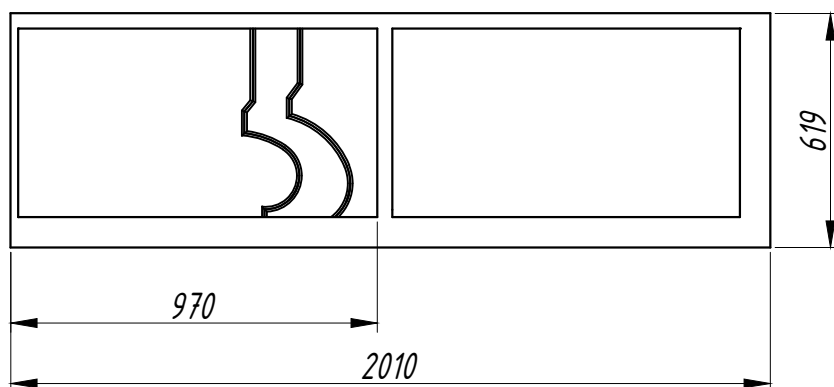




1. Является частью фронтальной стены.
2. Лайтбоксы крепятся друг к другу через болтовое соединение в единую стену.
3. Поясная сборка – от верхнего пояса к нижнему. После монтажа стена стоит на планшете сцены статично.
4. Каркас изготовить из металлопроката.
5. Облицовку затянуть транслюцентной баннерной тканью.
6. Чёрные полосы выполнить из тонкой фанеры (4–6 мм), внакладку по плоскости стенки, окрасить в матовый чёрный.
7. Необходимо предусмотреть быструю замену светопроницаемой ткани при её повреждении.
8. Предусмотреть места крепления светового оборудования, согласно техническому заданию художника по свету.

ТХОС 1.02.-00				"Молодожены" Богомолов К.						
	Фамилия	Подпись	Дата	Фронтальная стена. Лайтбокс 1-1.17 Габариты			Литера		Масса	Масштаб
Проверил	Галич.В.В.						у		Размеры	М 1:20
Принял	Галич.В.В.									
							Лист		Листов	
Чертил	Глухов И.А.			ГБУК г.Москвы "Театр на Малой Бронной"			Школа - студия МХАТ			

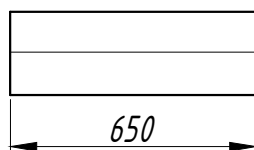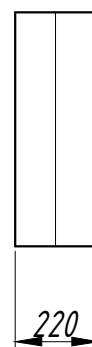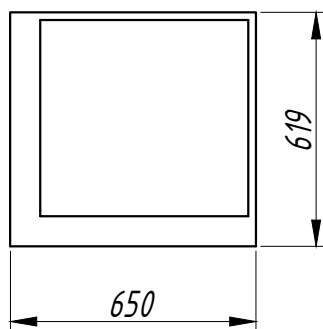




1. Является частью фронтальной стены.
2. Лайтбоксы крепятся друг к другу через болтовое соединение в единую стену.
3. Поясная сборка – от верхнего пояса к нижнему. После монтажа стена стоит на планшете сцены статично.
4. Каркас изготовить из металлопроката.
5. Облицовку натянуть транслюцентной баннерной тканью.
6. Чёрные полосы выполнить из тонкой фанеры (4–6 мм), внакладку по плоскости стенки, окрасить в матовый чёрный.
7. Необходимо предусмотреть быструю замену светопроницаемой ткани при её повреждении.
8. Предусмотреть места крепления светового оборудования, согласно техническому заданию художника по свету.

ТХОС 1.02.-00				"Молодожены" Богомолов К.						
	Фамилия	Подпись	Дата	Фронтальная стена. Лайтбокс 1-1.18 Габариты			Литера		Масса	Масштаб
Проверил	Галич.В.В.						у			М 1:20
									Размеры	
Принял	Галич.В.В.									
							Лист		Листов	
Чертил	Глухов И.А.			ГБУК г.Москвы "Театр на Малой Бронной"			Школа - студия МХАТ			

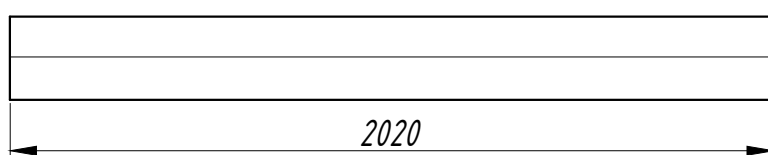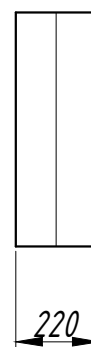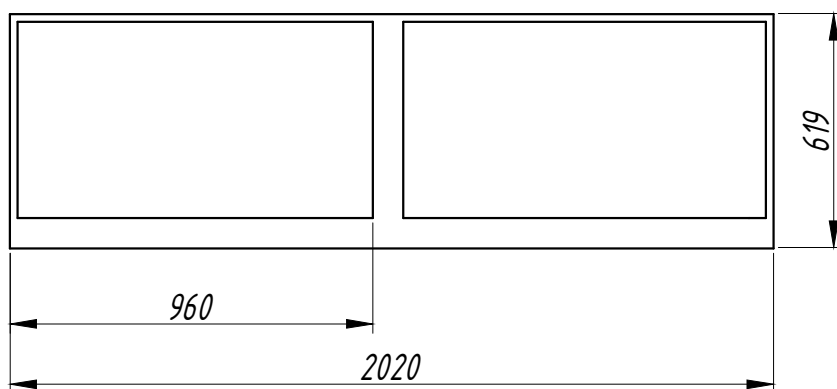

1. Является частью фронтальной стены.
2. Лайтбоксы крепятся друг к другу через болтовое соединение в единую стену.
3. Поясная сборка – от верхнего пояса к нижнему. После монтажа стена стоит на планшете сцены статично.
4. Каркас изготовить из металлопроката.
5. Облицовку затянуть translucentной баннерной тканью.
6. Чёрные полосы выполнить из тонкой фанеры (4–6 мм), внакладку по плоскости стенки, окрасить в матовый чёрный.
7. Необходимо предусмотреть быструю замену светопроницаемой ткани при её повреждении.
8. Предусмотреть места крепления светового оборудования, согласно техническому заданию художника по свету.

ТХОС 1.02.-00				"Молодожены" Богомолов К.			
	Фамилия	Подпись	Дата	Фронтальная стена. Лайтбокс 1-1.19 Габариты	Литера	Масса	Масштаб
Проверил	Галич.В.В.				у	Размеры	М 1:20
Принял	Галич.В.В.						
					Лист	Листов	
Чертил	Глухов И.А.			ГБУК г.Москвы "Театр на Малой Бронной"	Школа - студия МХАТ		

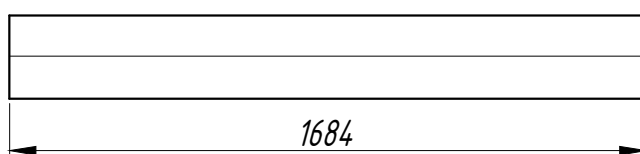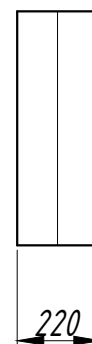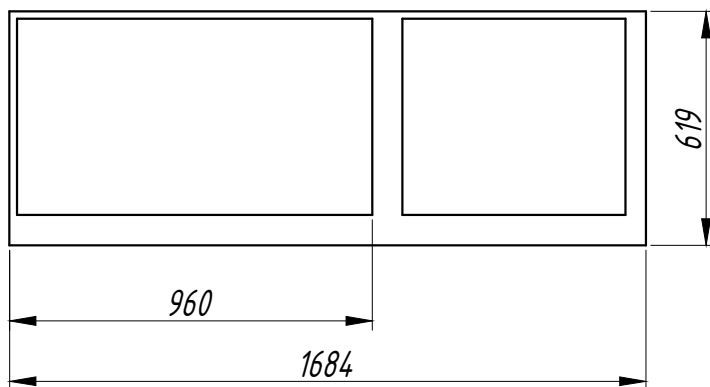

1. Является частью фронтальной стены.
2. Лайтбоксы крепятся друг к другу через болтовое соединение в единую стену.
3. Поясная сборка – от верхнего пояса к нижнему. После монтажа стена стоит на планшете сцены статично.
4. Каркас изготовить из металлопроката.
5. Облицовку затянуть транслюцентной баннерной тканью.
6. Чёрные полосы выполнить из тонкой фанеры (4–6 мм), внакладку по плоскости стенки, окрасить в матовый чёрный.
7. Необходимо предусмотреть быструю замену светопроницаемой ткани при её повреждении.
8. Предусмотреть места крепления светового оборудования, согласно техническому заданию художника по свету.

ТХОС 1.02.-00				"Молодожены" Богомолов К.							
	Фамилия	Подпись	Дата	Фронтальная стена. Лайтбокс 1-1.20 Габариты			Литера		Масса	Масштаб	
Проверил	Галич .В .В .							у		Размеры	М 1:20
Принял	Галич .В .В .										
Чертил	Глухов И.А.			ГБУК г.Москвы "Театр на Малой Бронной"			Лист		Листов		
							Школа - студия МХАТ				



** – размер для справки.*

1 Каркас выполнить из металлопроката.



2 В углах силового каркаса лайтбокса установить стаканы для ног (под профильную трубу 50х50 мм). Ноги съёмные, хранятся отдельно.

3 Настила – монолитный поликарбонат 15 мм

4 Лайтбоксы крепятся друг к другу на болтовом соединении.

5 Предусмотреть места крепления светового оборудования, согласно техническому заданию художника по свету.

ТХОС 1.02.-1-2				"Молодожены" Богомолов К.					
	Фамилия	Подпись	Дата	Станок 1000 х 350. Габариты. 9 шт.	Литера		Масса	Масштаб	
Проверил	Галич.В.В.				у			М 1:20	
							Размеры		
Принял	Галич.В.В.								
					Лист		Листов		
Чертил	Глухов И.А.			ГБУК г.Москвы "Театр на Малой Бронной"		Школа - студия МХАТ			

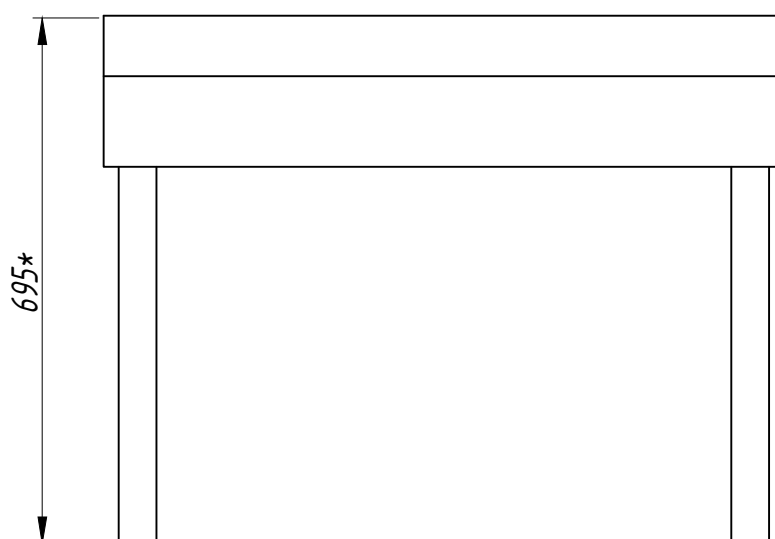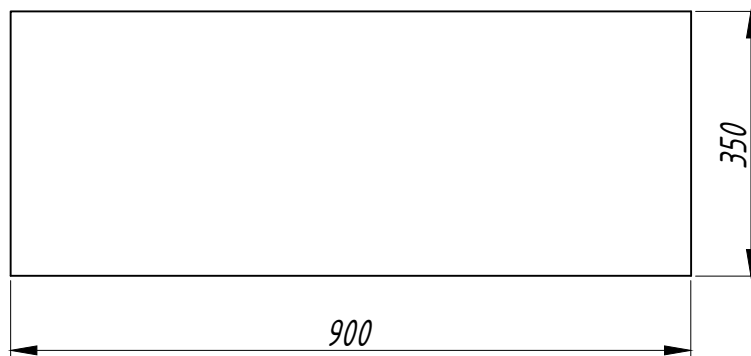

** – размер для справки.*

1 Каркас выполнить из металлопроката.


2 В углах силового каркаса лайтбокса установить стаканы для ног (под профильную трубу 50х50 мм). Ноги съёмные, хранятся отдельно.

3 Настила – монолитный поликарбонат 15 мм

4 Лайтбоксы крепятся друг к другу на болтовом соединении.

5 Предусмотреть места крепления светового оборудования, согласно техническому заданию художника по свету.

ТХОС 1.02.-1-3				"Молодожены" Богомолов К.						
	Фамилия	Подпись	Дата	Станок 900 х 350. Габариты. 2 шт.			Литера		Масса	Масштаб
Проверил	Галич .В .В .						у			М 1:10
									Размеры	
Принял	Галич .В .В .									
							Лист		Листов	
Чертил	Глухов И.А.			ГБУК г.Москвы "Театр на Малой Бронной"			Школа - студия МХАТ			

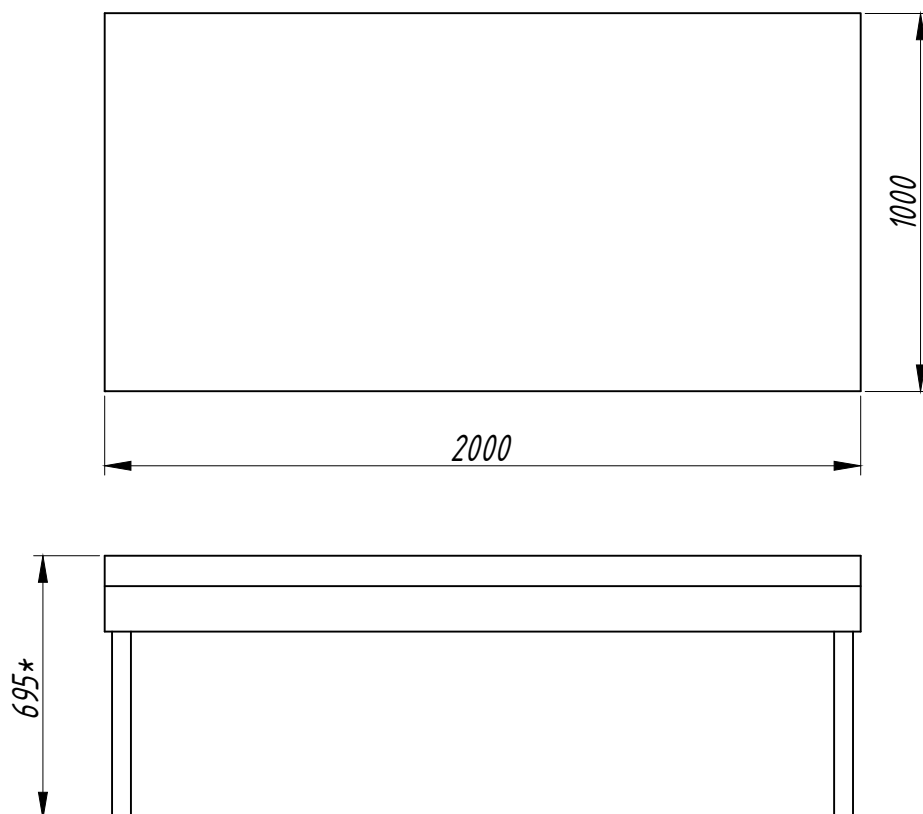

** – размер для справки.*

1 Каркас выполнить из металлопроката.


2 В углах силового каркаса лайтбокса установить стаканы для ног (под профильную трубу 50х50 мм). Ноги съёмные, хранятся отдельно.

3 Настила – монолитный поликарбонат 15 мм

4 Лайтбоксы крепятся друг к другу на болтовом соединении.

5 Предусмотреть места крепления светового оборудования, согласно техническому заданию художника по свету.

ТХОС 1.02.-1-4				"Молодожены" Богомолов К.						
	Фамилия	Подпись	Дата	Станок 1000 x 2000. Габариты. 9 шт.			Литера		Масса	Масштаб
Проверил	Галич.В.В.						у			М 1:20
									Размеры	
Принял	Галич.В.В.									
							Лист		Листов	
Чертил	Глухов И.А.			ГБУК г.Москвы "Театр на Малой Бронной"			Школа - студия МХАТ			

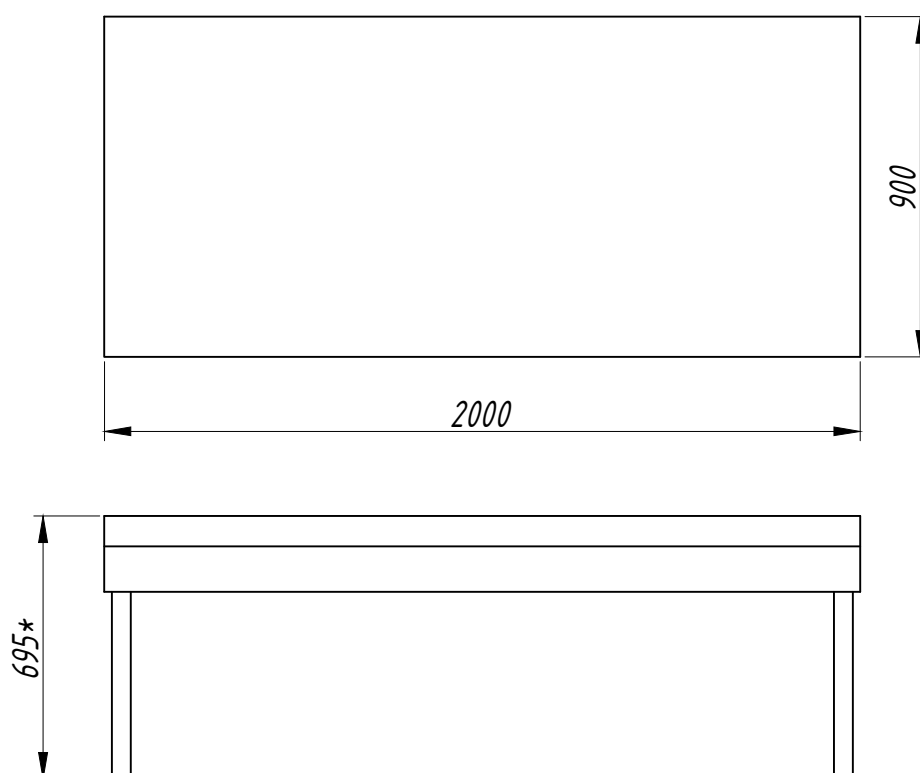

* – размер для справки.

1 Каркас выполнить из металлопроката.



2 В углах силового каркаса лайтбокса установить стаканы для ног (под профильную трубу 50х50 мм). Ноги съёмные, хранятся отдельно.

3 Настила – монолитный поликарбонат 15 мм

4 Лайтбоксы крепятся друг к другу на болтовом соединении.



5 Предусмотреть места крепления светового оборудования, согласно техническому заданию художника по свету.

ТХОС 1.02.-1-5				"Молодожены" Богомолов К.						
	Фамилия	Подпись	Дата	Станок 900 х 2000. Габариты. 2 шт.			Литера		Масса	Масштаб
Проверил	Галич.В.В.						у			М 1:20
								Размеры		
Принял	Галич.В.В.									
							Лист		Листов	
Чертил	Глухов И.А.			ГБУК г.Москвы "Театр на Малой Бронной"			Школа - студия МХАТ			

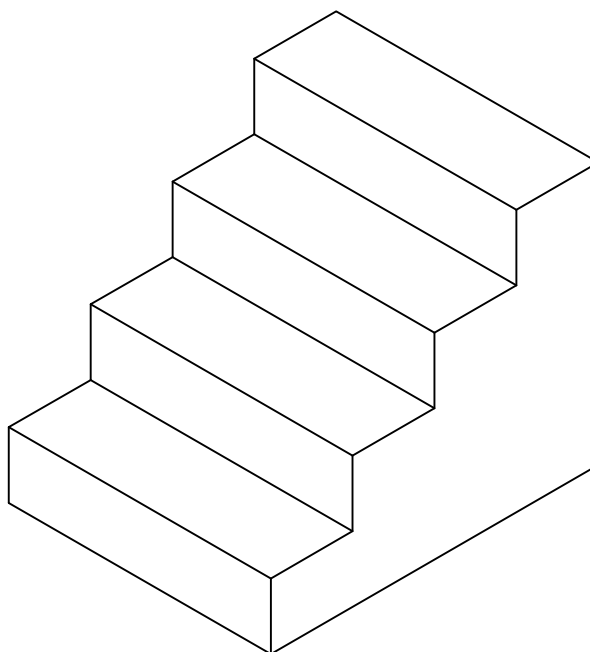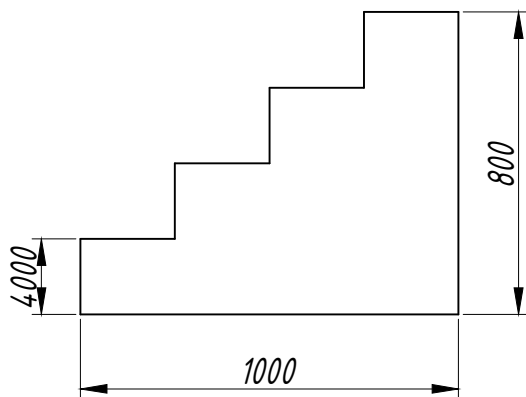


- 1 Каркас выполнить из металлопроката.
- 2 Ступени зашить фанерой 10 мм.
- 3 Подступенок и доковины зашить фанерой 6 мм.
- 4 Покрасить в чёрный цвет.

ТХОС 1.02.-1-6				"Молодожены" Богомолов К.						
	Фамилия	Подпись	Дата	Лестница Н 800 х 800 х 1000. Габариты. 2 шт.	Литера		Масса	Масштаб		
Проверил	Галич.В.В.				у			М 1:20		
						Размеры				
Принял	Галич.В.В.									
					Лист		Листов			
Чертил	Глухов И.А.				ГБУК г.Москвы "Театр на Малой Бронной"		Школа - студия МХАТ			

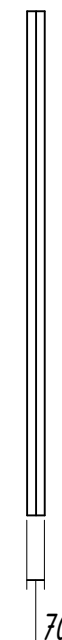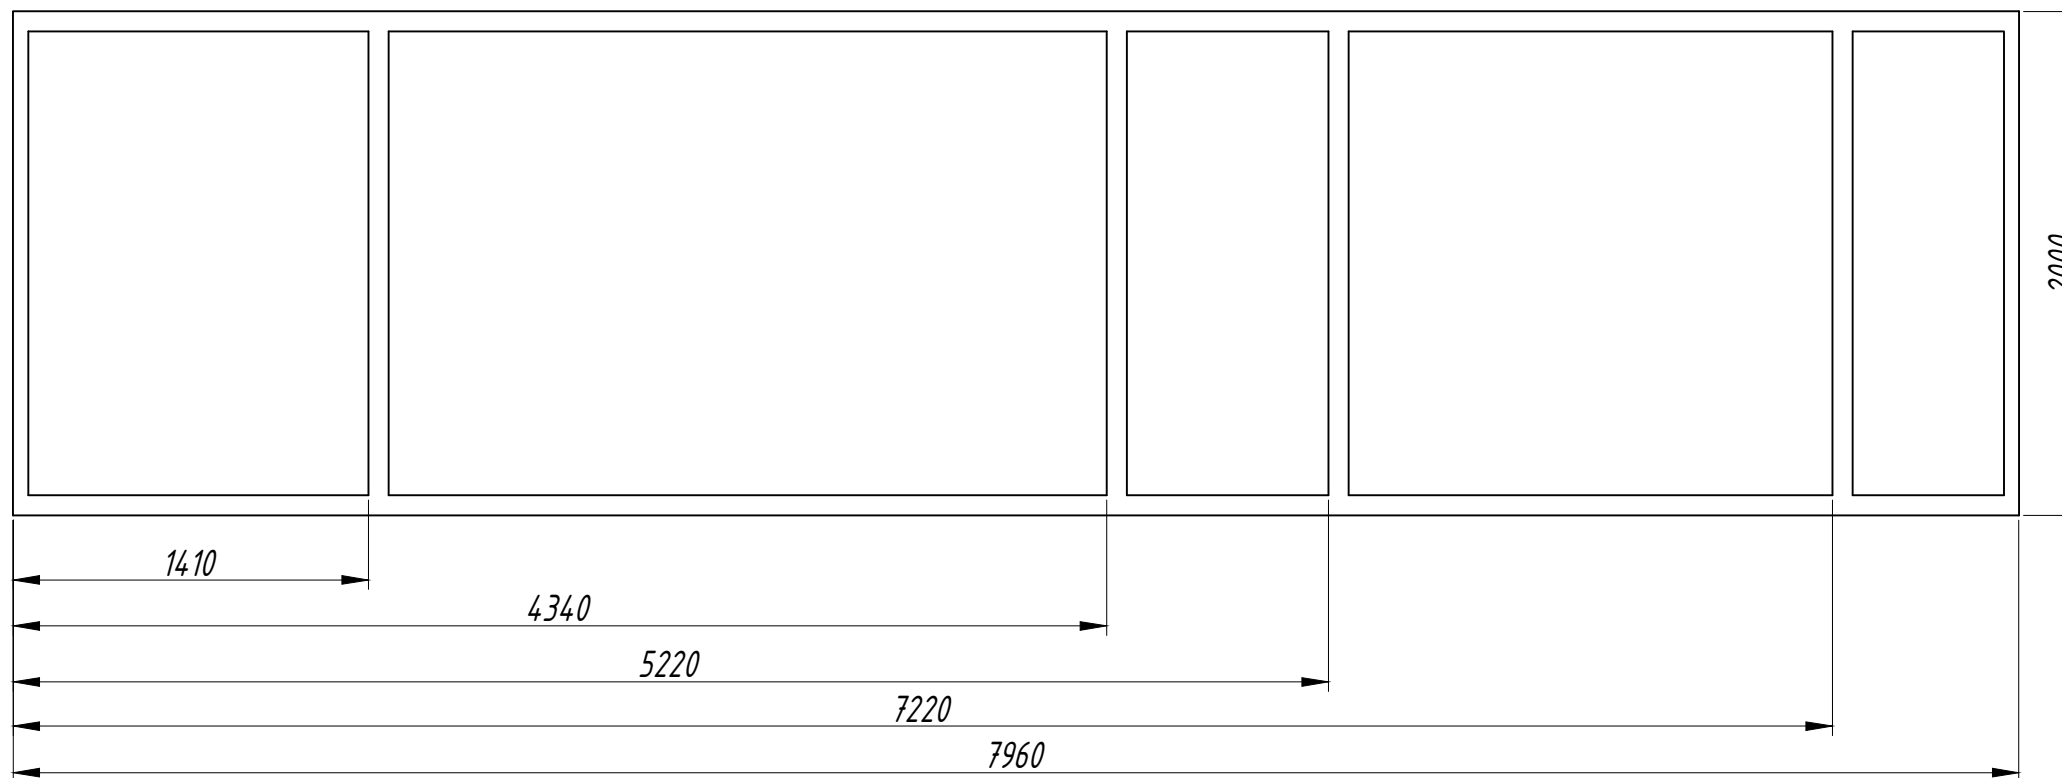


1. Плоская разборная конструкция.
2. Каркас – металл/алюминиевый профиль
3. Потолок устанавливается внутри проёма архитектурного портала сцены сверху, между двумя порталными стенками. Передний край стенки установить вровень с порталной стеной театра. Потолок левым и правым краями «лежит» на верхних кромках боковых порталных стенок, образуя с ними единую П-образную конструкцию.
4. Необходимо предусмотреть крепления потолка к порталным стенкам и к стационарным конструкциям театра для фиксации средней части пролёта потолка во избежание провиса по длине. Возможно использование штанкетов авансцены и нулевого плана для подъёма потолка на необходимую высоту. По переднему краю потолок можно зафиксировать к каркасу порталной решётки.
5. Чёрные полосы выполнить из тонкой фанеры (4–6 мм), внакладку по плоскости стенки; окрасить в матовый чёрный.
6. Основную плоскость потолка декорировать под фактуру гладкой штукатурки

ТХОС 1.02.-1-7				"Молодожены" Богомолов К.			
	Фамилия	Подпись	Дата	Потолок . Габариты .	Литера	Масса	Масштаб
Проверил	Галич.В.В.				у		М 1:30
Принял	Галич.В.В.					Размеры	
Чертил	Глухов И.А.			ГБУК г.Москвы "Театр на Малой Бронной"	Лист		Листов
					Школа -студия МХАТ		

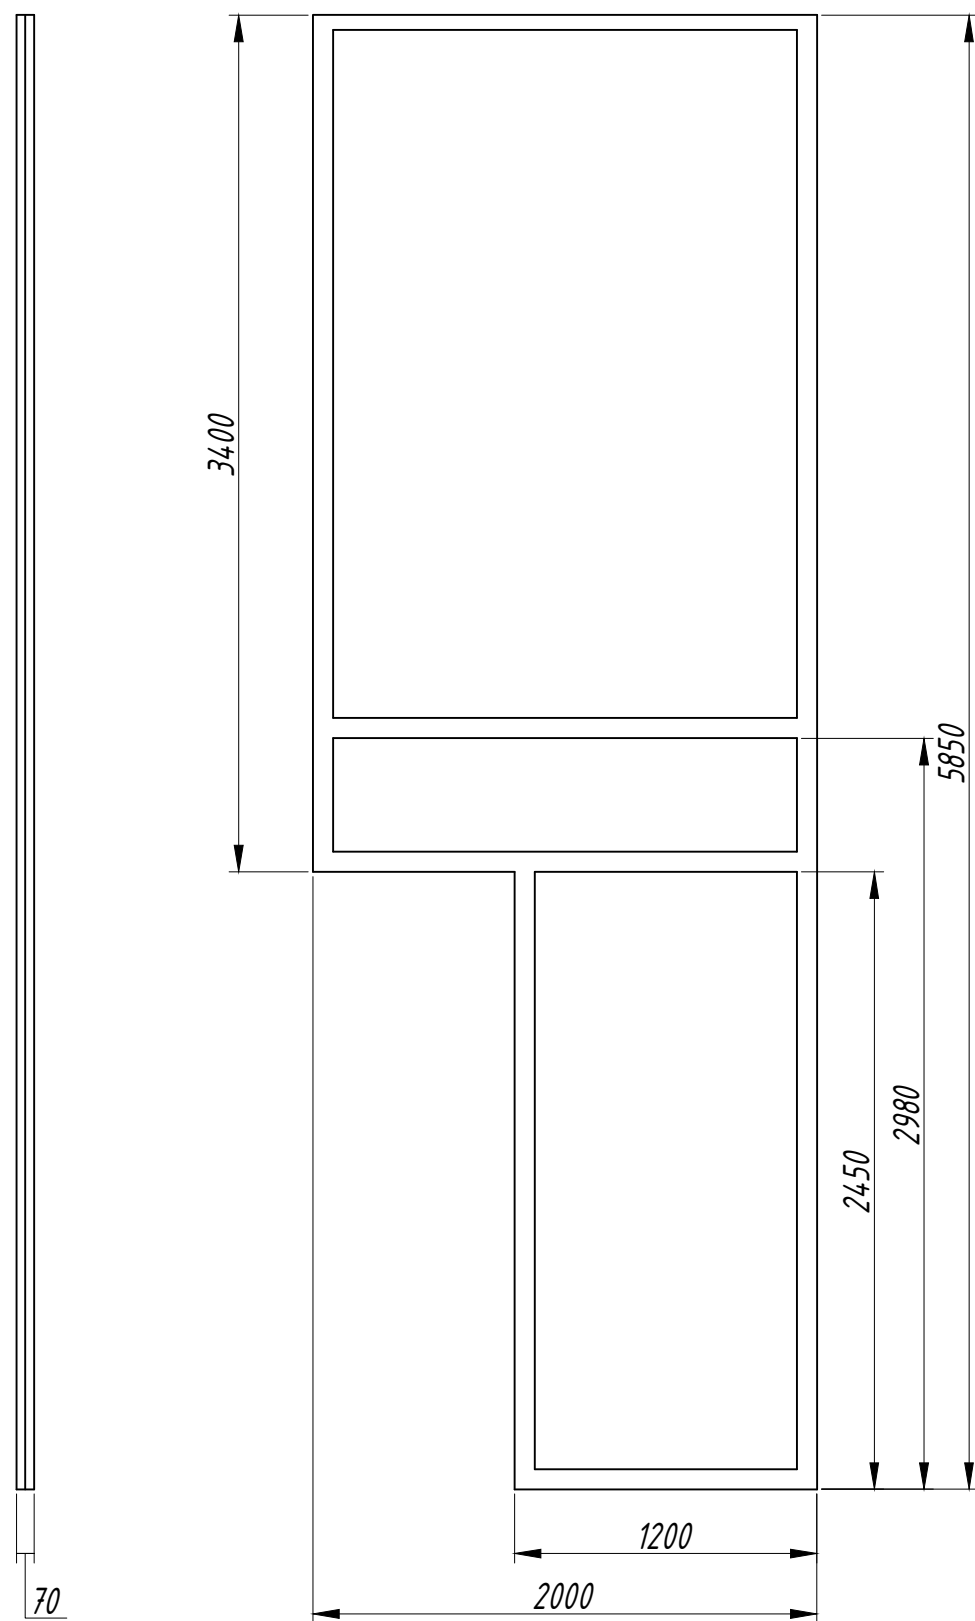


- Стенка порталная правая устанавливается внутри проёма архитектурного портала сцены справа, перпендикулярно линии авансцены.
1. Плоская разборная конструкция. Делить на 2 (возможно 3) части, ближе к центру стены, стык выполнить по черной декоративной накладке.
 2. Каркас – металл/алюминиевый профиль
 3. Передний край стенки установить вровень с порталной стеной театра.
 4. По низу стенки предусмотреть крепления саморезами к планшету сцены.
 5. По верху стенки – соединение с «Потолком».
 6. Чёрные полосы выполнить из тонкой фанеры (4–6 мм), внакладку по плоскости стенки; окрасить в матовый чёрный.
 7. Основную плоскость стенки декорировать под фактуру гладкой штукатурки.

ТХОС 1.02.-1-8				"Молодожены" Богомолов К.			
	Фамилия	Подпись	Дата	Стена правая. Габариты.	Литера	Масса	Масштаб
Проверил	Галич.В.В.				У		М 1:30
						Размеры	
Принял	Галич.В.В.						
				ГБУК г.Москвы "Театр на Малой Бронной"	Лист		Листов
Чертил	Глухов И.А.				Школа -студия МХАТ		

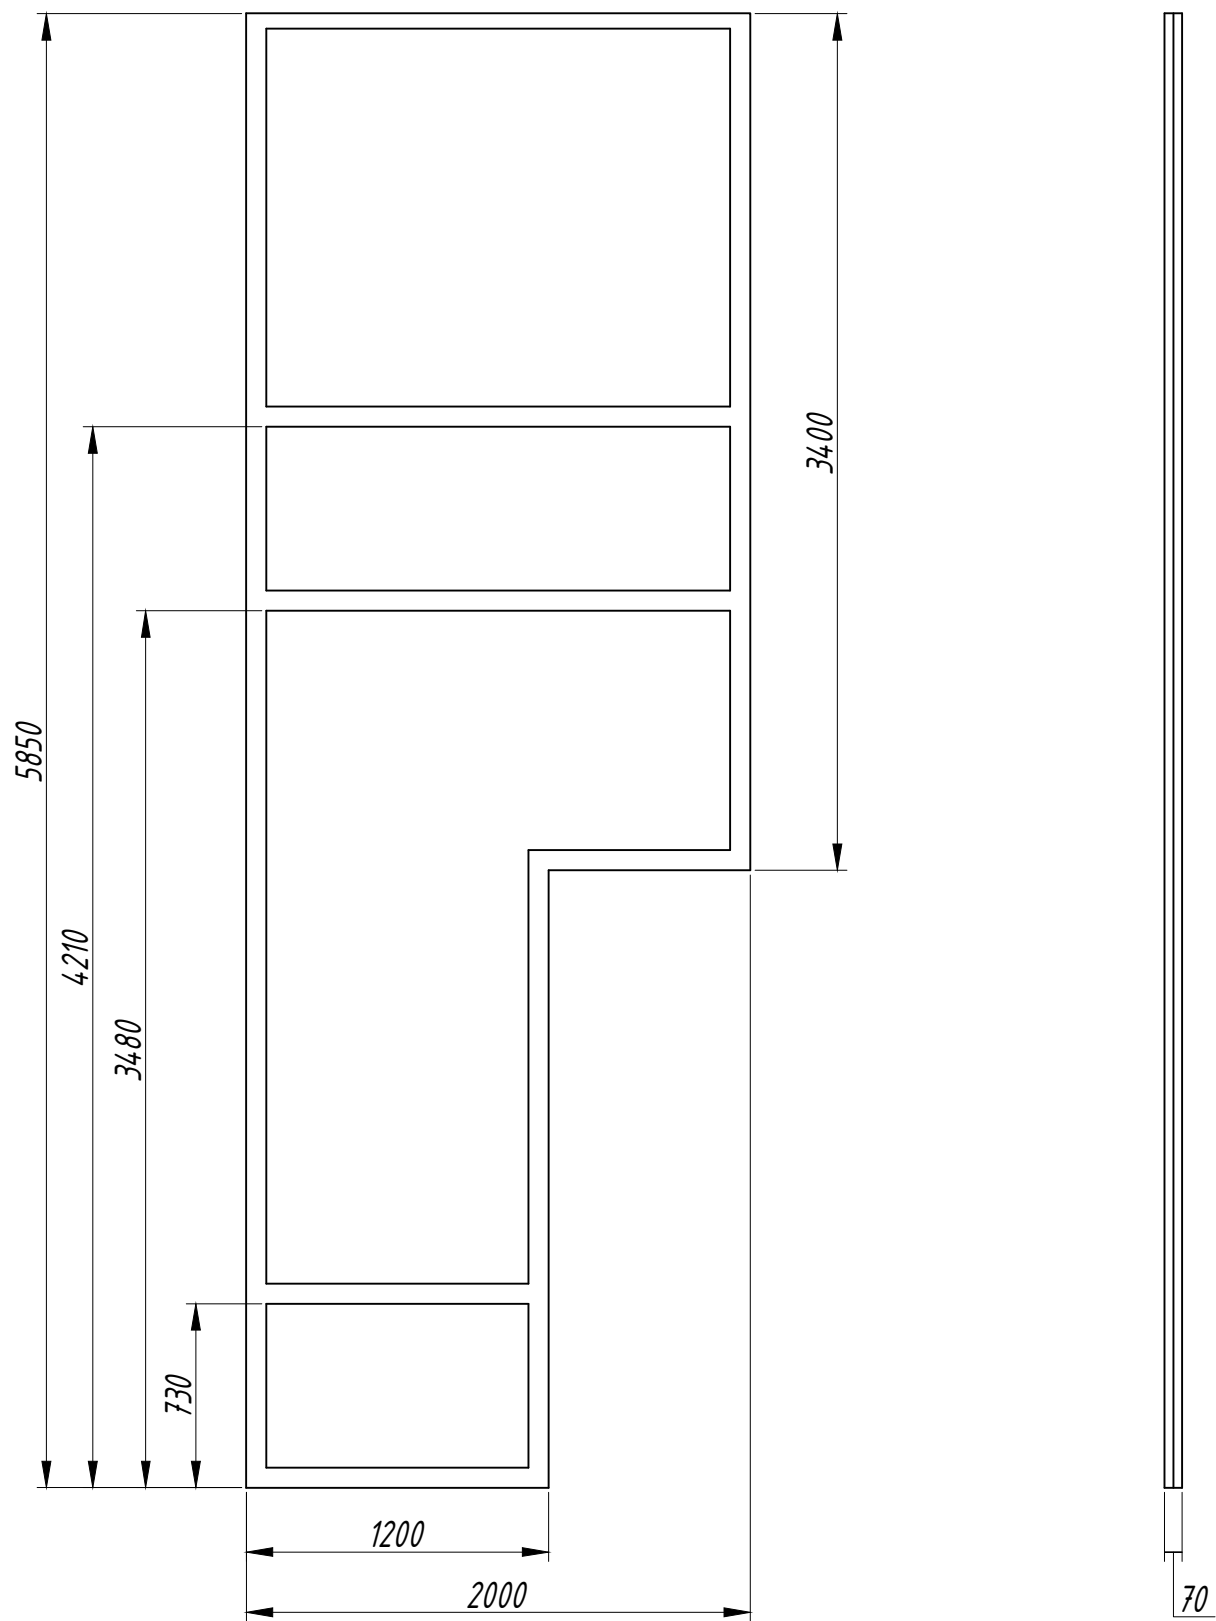


- Стенка порталная левая устанавливается внутри проёма архитектурного портала сцены слева, перпендикулярно линии авансцены.
1. Плоская разборная конструкция. Делить на 2 (возможно 3) части, ближе к центру стены, стык выполнить по черной декоративной накладке.
 2. Каркас – металл/алюминиевый профиль
 3. Передний край стенки установить вровень с порталной стеной театра.
 4. По низу стенки предусмотреть крепления саморезами к планшету сцены.
 5. По верху стенки – соединение с «Потолком».
 6. Чёрные полосы выполнить из тонкой фанеры (4–6 мм), внакладку по плоскости стенки; окрасить в матовый чёрный.
 7. Основную плоскость стенки декорировать под фактуру гладкой штукатурки.

ТХОС 1.02.-1-9				"Молодожены" Богомолов К.			
	Фамилия	Подпись	Дата	Стена левая. Габариты.	Литера	Масса	Масштаб
Проверил	Галич.В.В.				У	Размеры	М 1:30
Принял	Галич.В.В.						
Чертил	Глухов И.А.				Лист	Листов	
				ГБУК г.Москвы "Театр на Малой Бронной"	Школа -студия МХАТ		

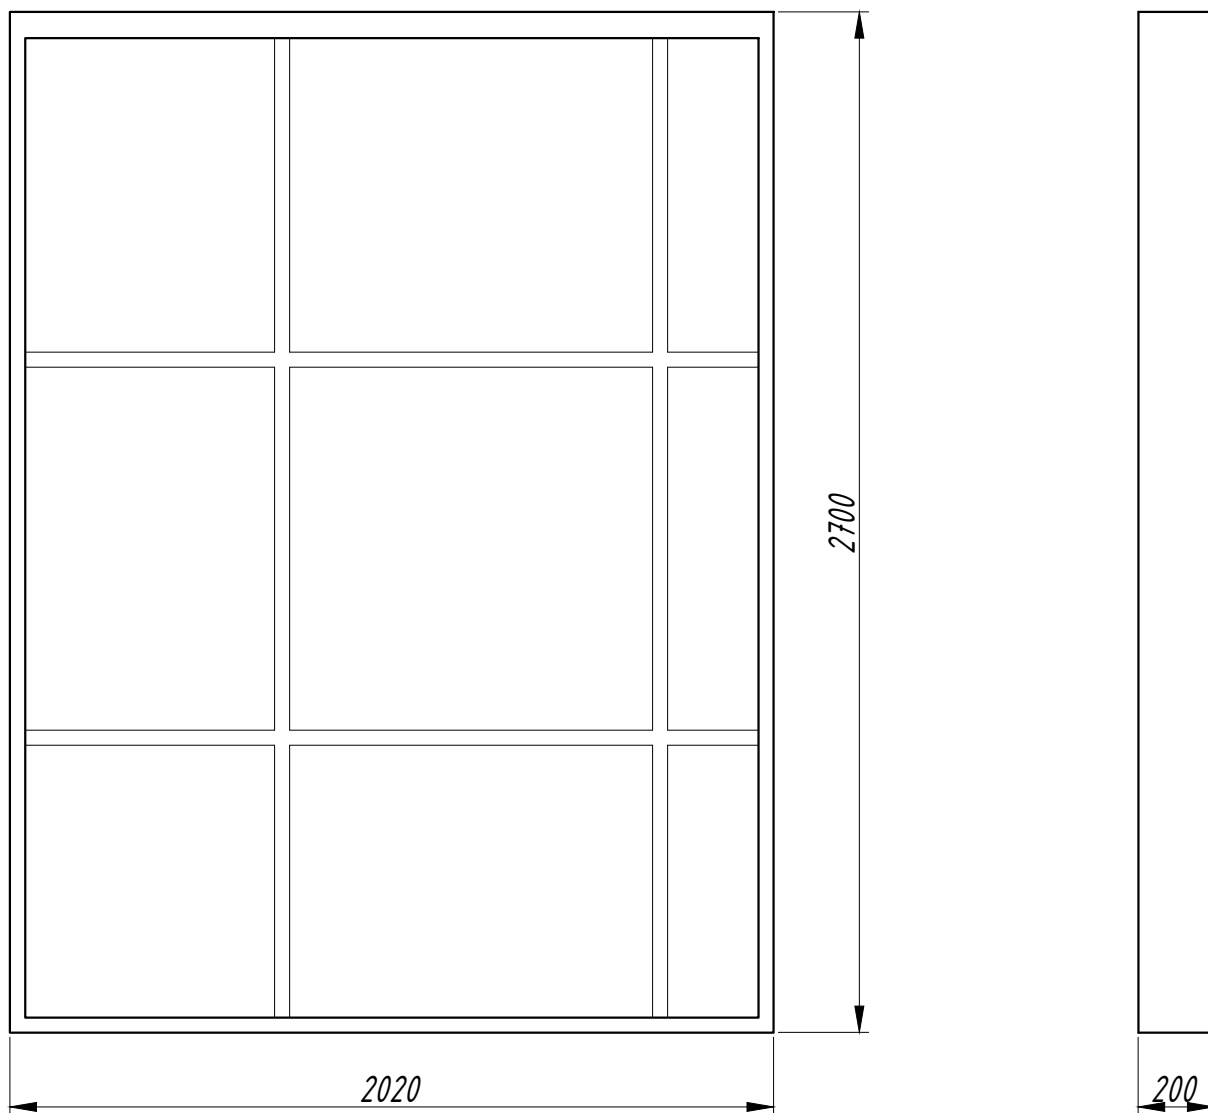

ТХОС 1.02.-1-12				"Молодожены" Богомолов К.						
	Фамилия	Подпись	Дата	Афиша . Н 2700 x 2020 x 200. Габариты .			Литера		Масса	Масштаб
Проверил	Галич .В .В .						у	Размеры		М 1:20
Принял	Галич .В .В .									
				Лист		Листов				
Чертил	Глухов И.А.			ГБУК г.Москвы "Театр на Малой Бронной"			Школа - студия МХАТ			

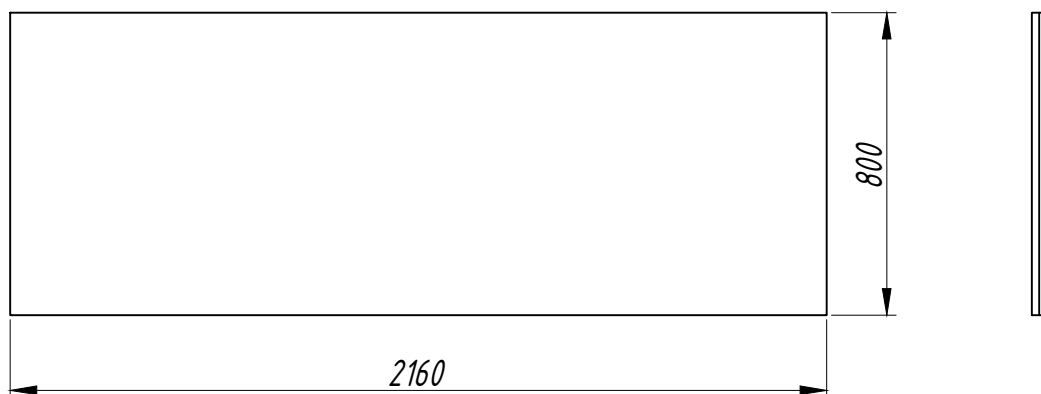


Представляет собой металлическую рамку, обтянутую чёрным сукном.

1. Плоская разборная конструкция.

2. Габарит обусловлен длиной и высотой выносного станка

3. Предусмотреть крепление к выносному станку.

ТХОС 1.02.-00				"Молодожены" Богомолов К.						
	Фамилия	Подпись	Дата	Раус. Габариты. 5 шт.			Литера		Масса	Масштаб
Проверил	Галич.В.В.						у			М 1:20
									Размеры	
Принял	Галич.В.В.									
							Лист		Листов	
Чертил	Глухов И.А.			ГБУК г.Москвы "Театр на Малой Бронной"			Школа - студия МХАТ			

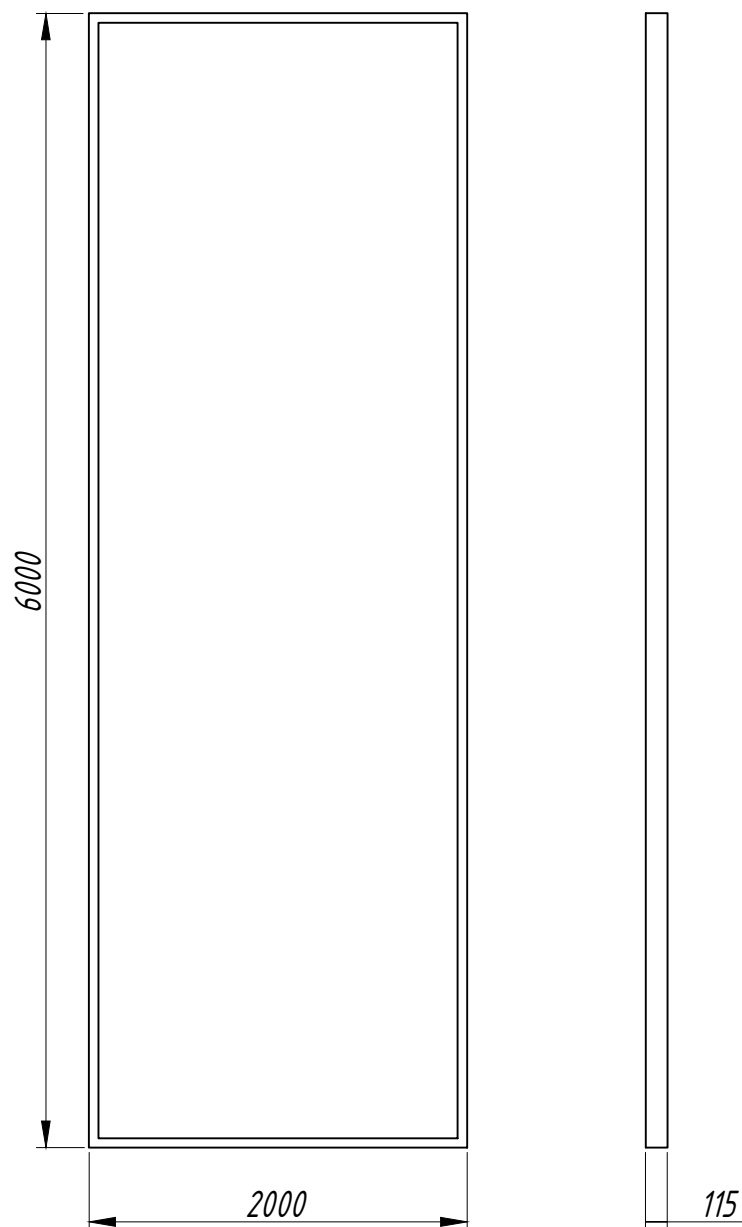

ТХОС 1.02.-1-12				"Молодожены" Богомолов К.						
	Фамилия	Подпись	Дата	Портальные экраны H 6000 x 1600. Габариты. 2 шт.			Литера		Масса	Масштаб
Проверил	Галич.В.В.						у			М 1:40
									Размеры	
Принял	Галич.В.В.									
							Лист		Листов	
Чертил	Глухов И.А.			ГБУК г.Москвы "Театр на Малой Бронной"			Школа - студия МХАТ			