
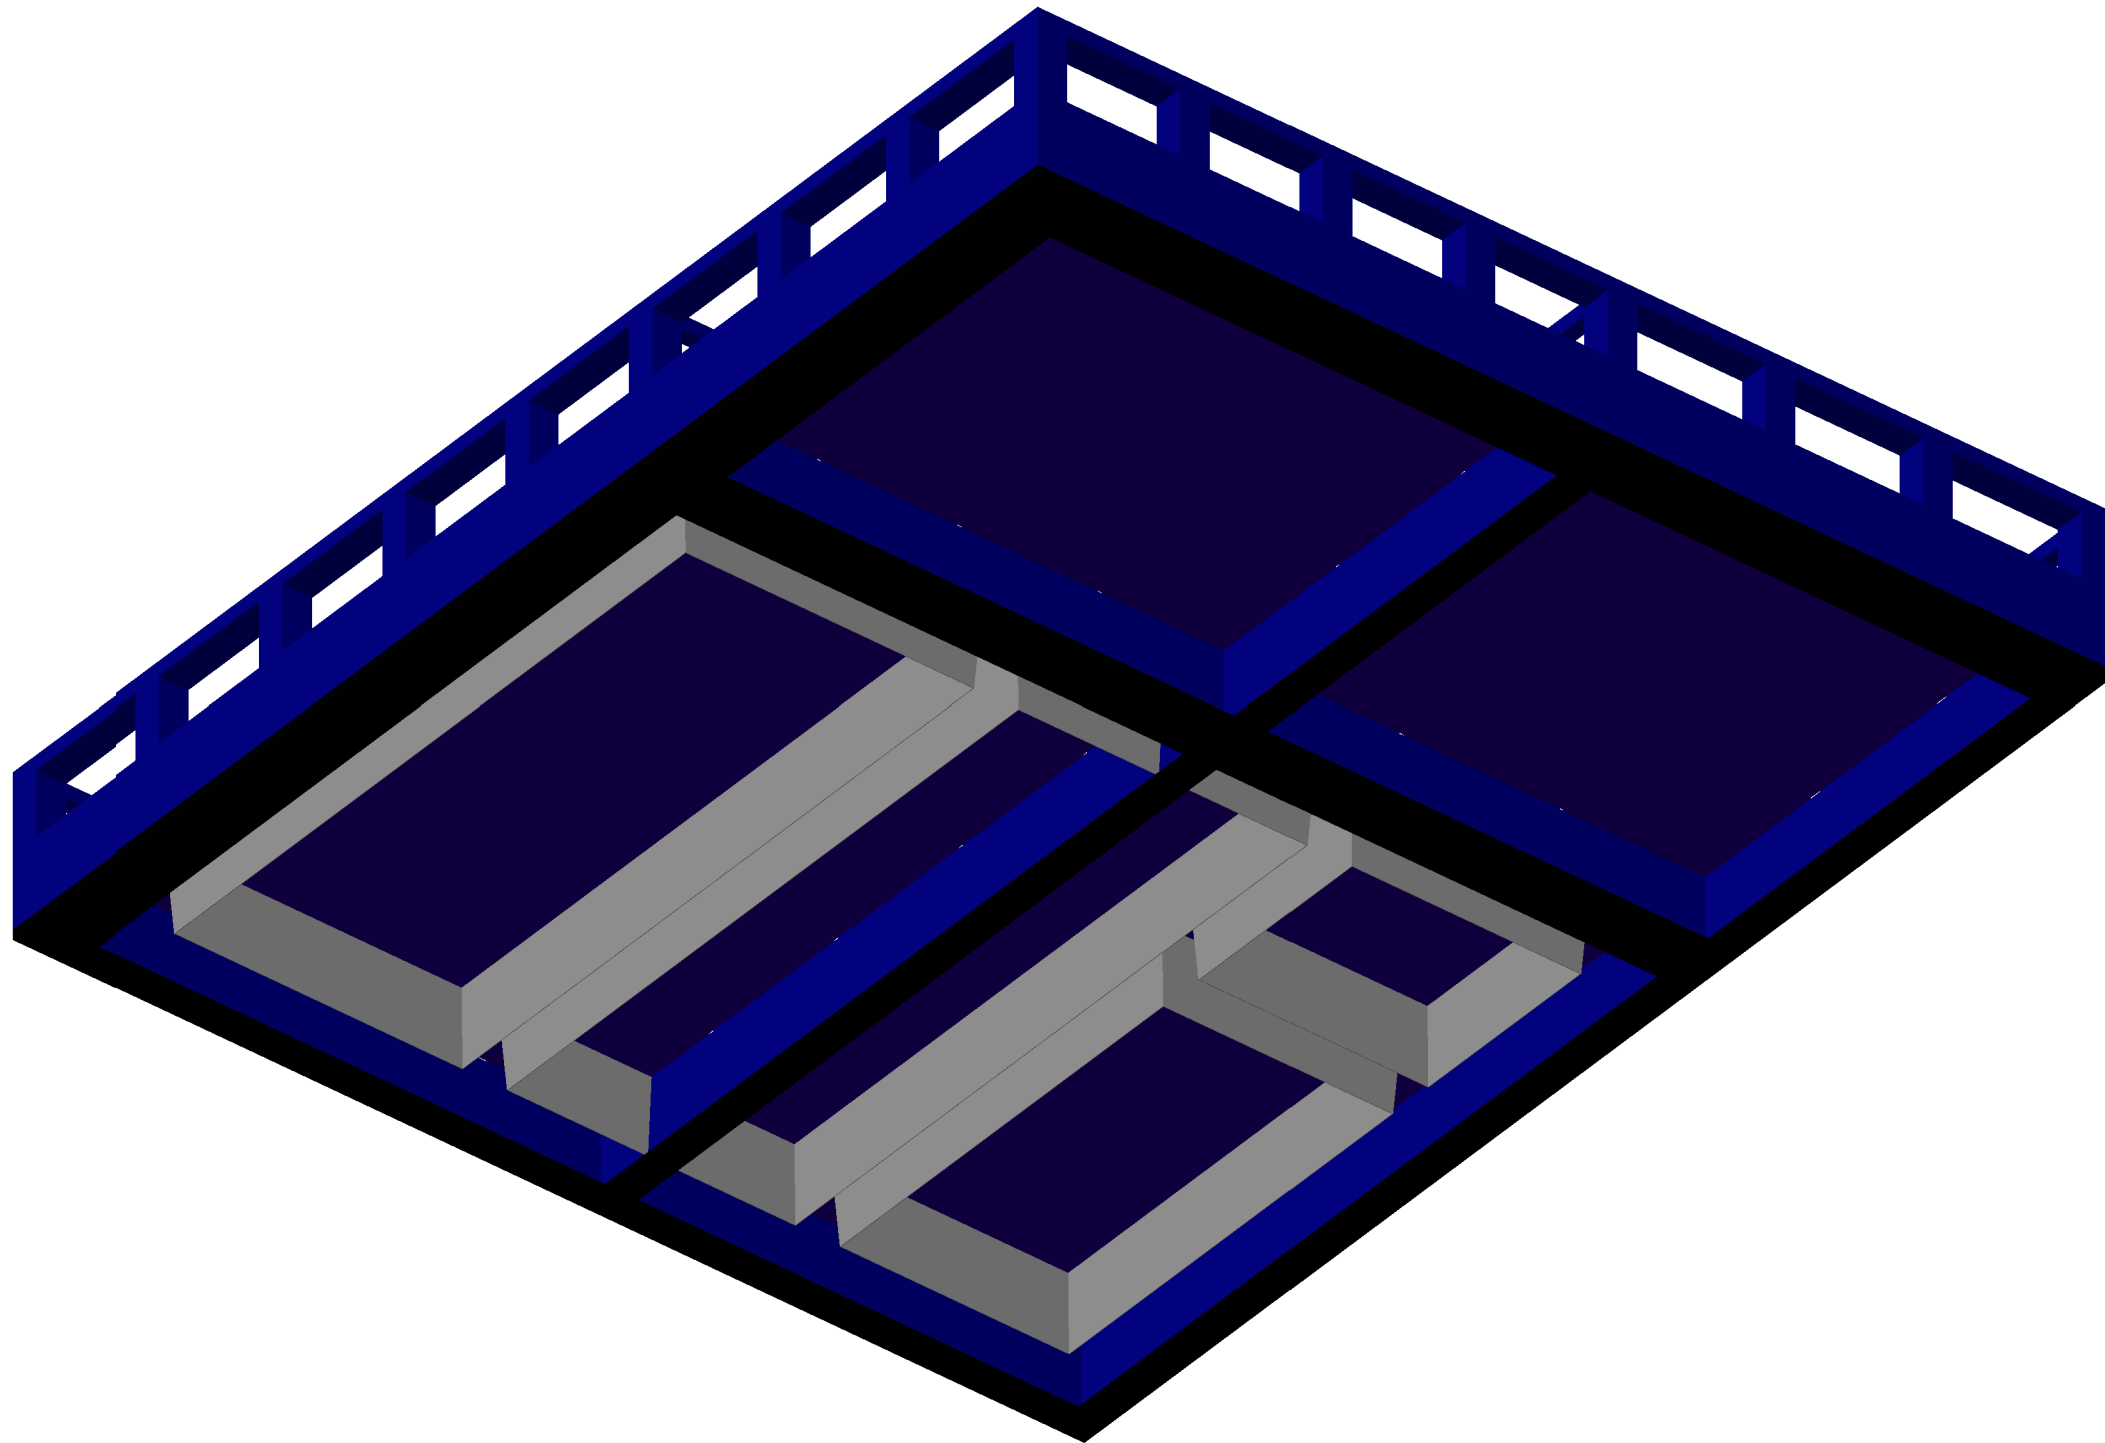
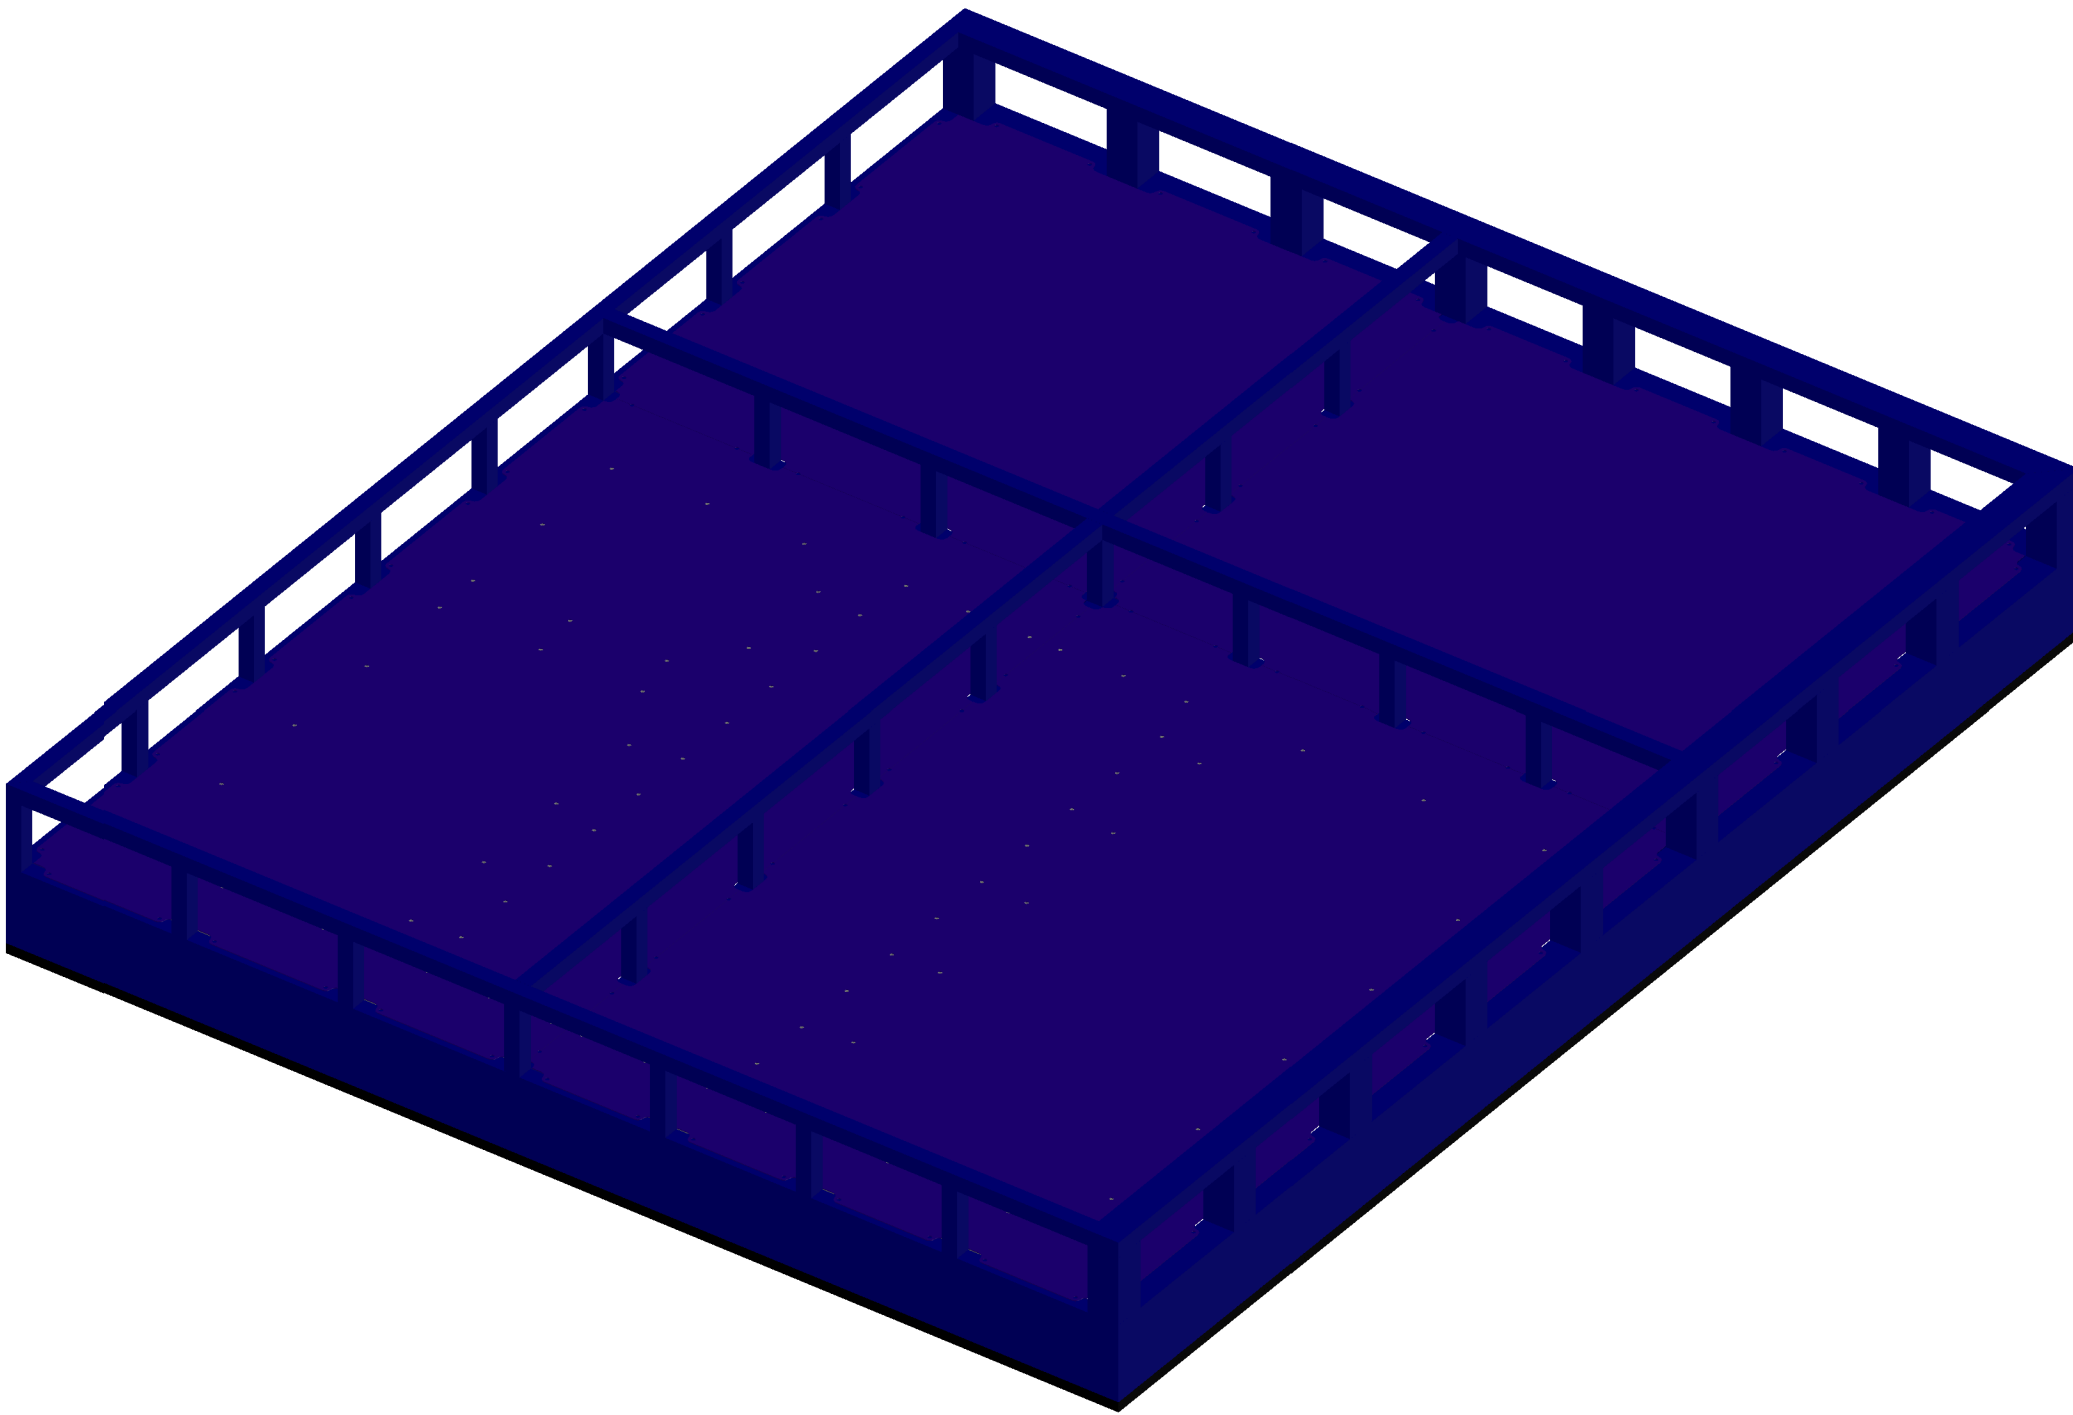
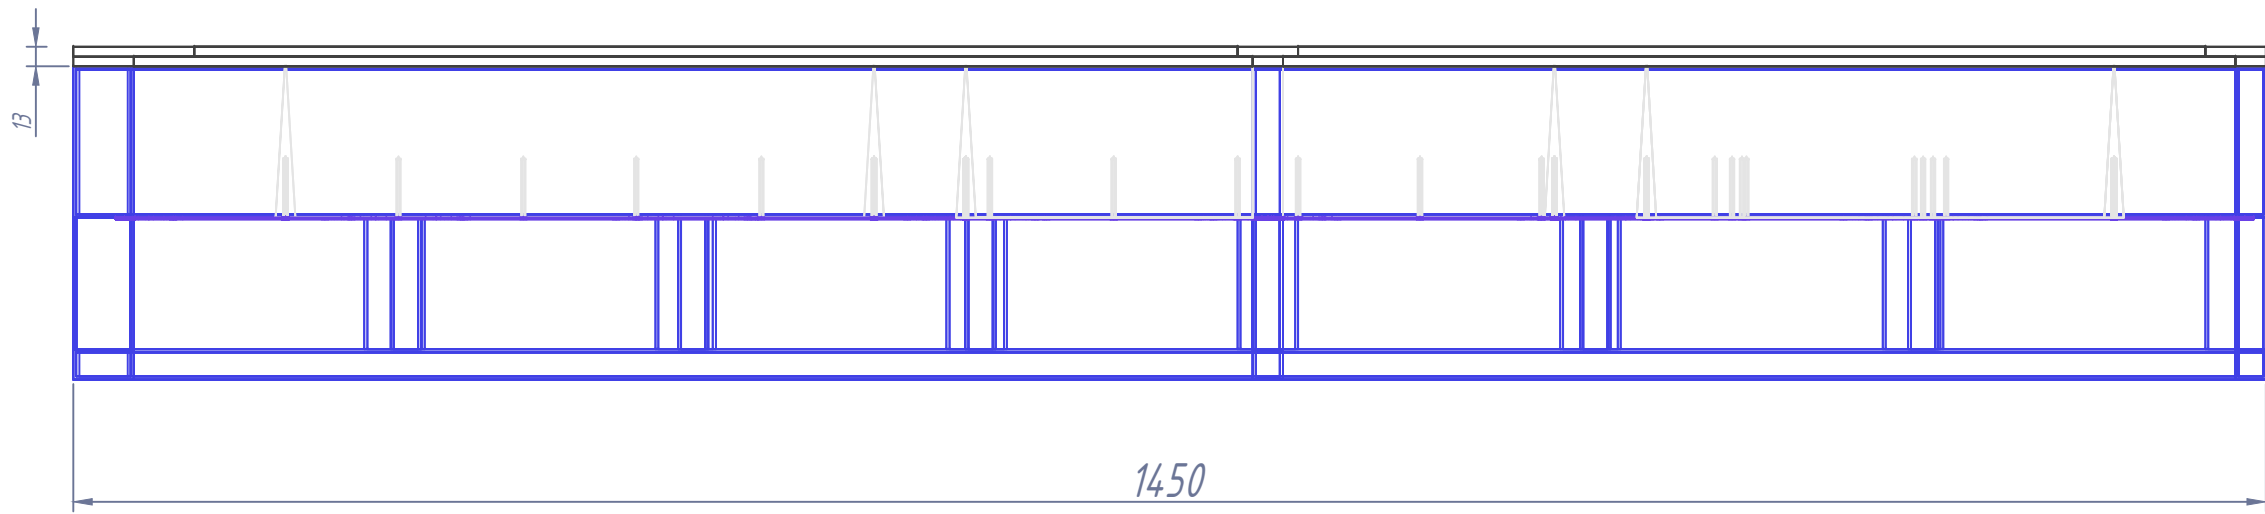


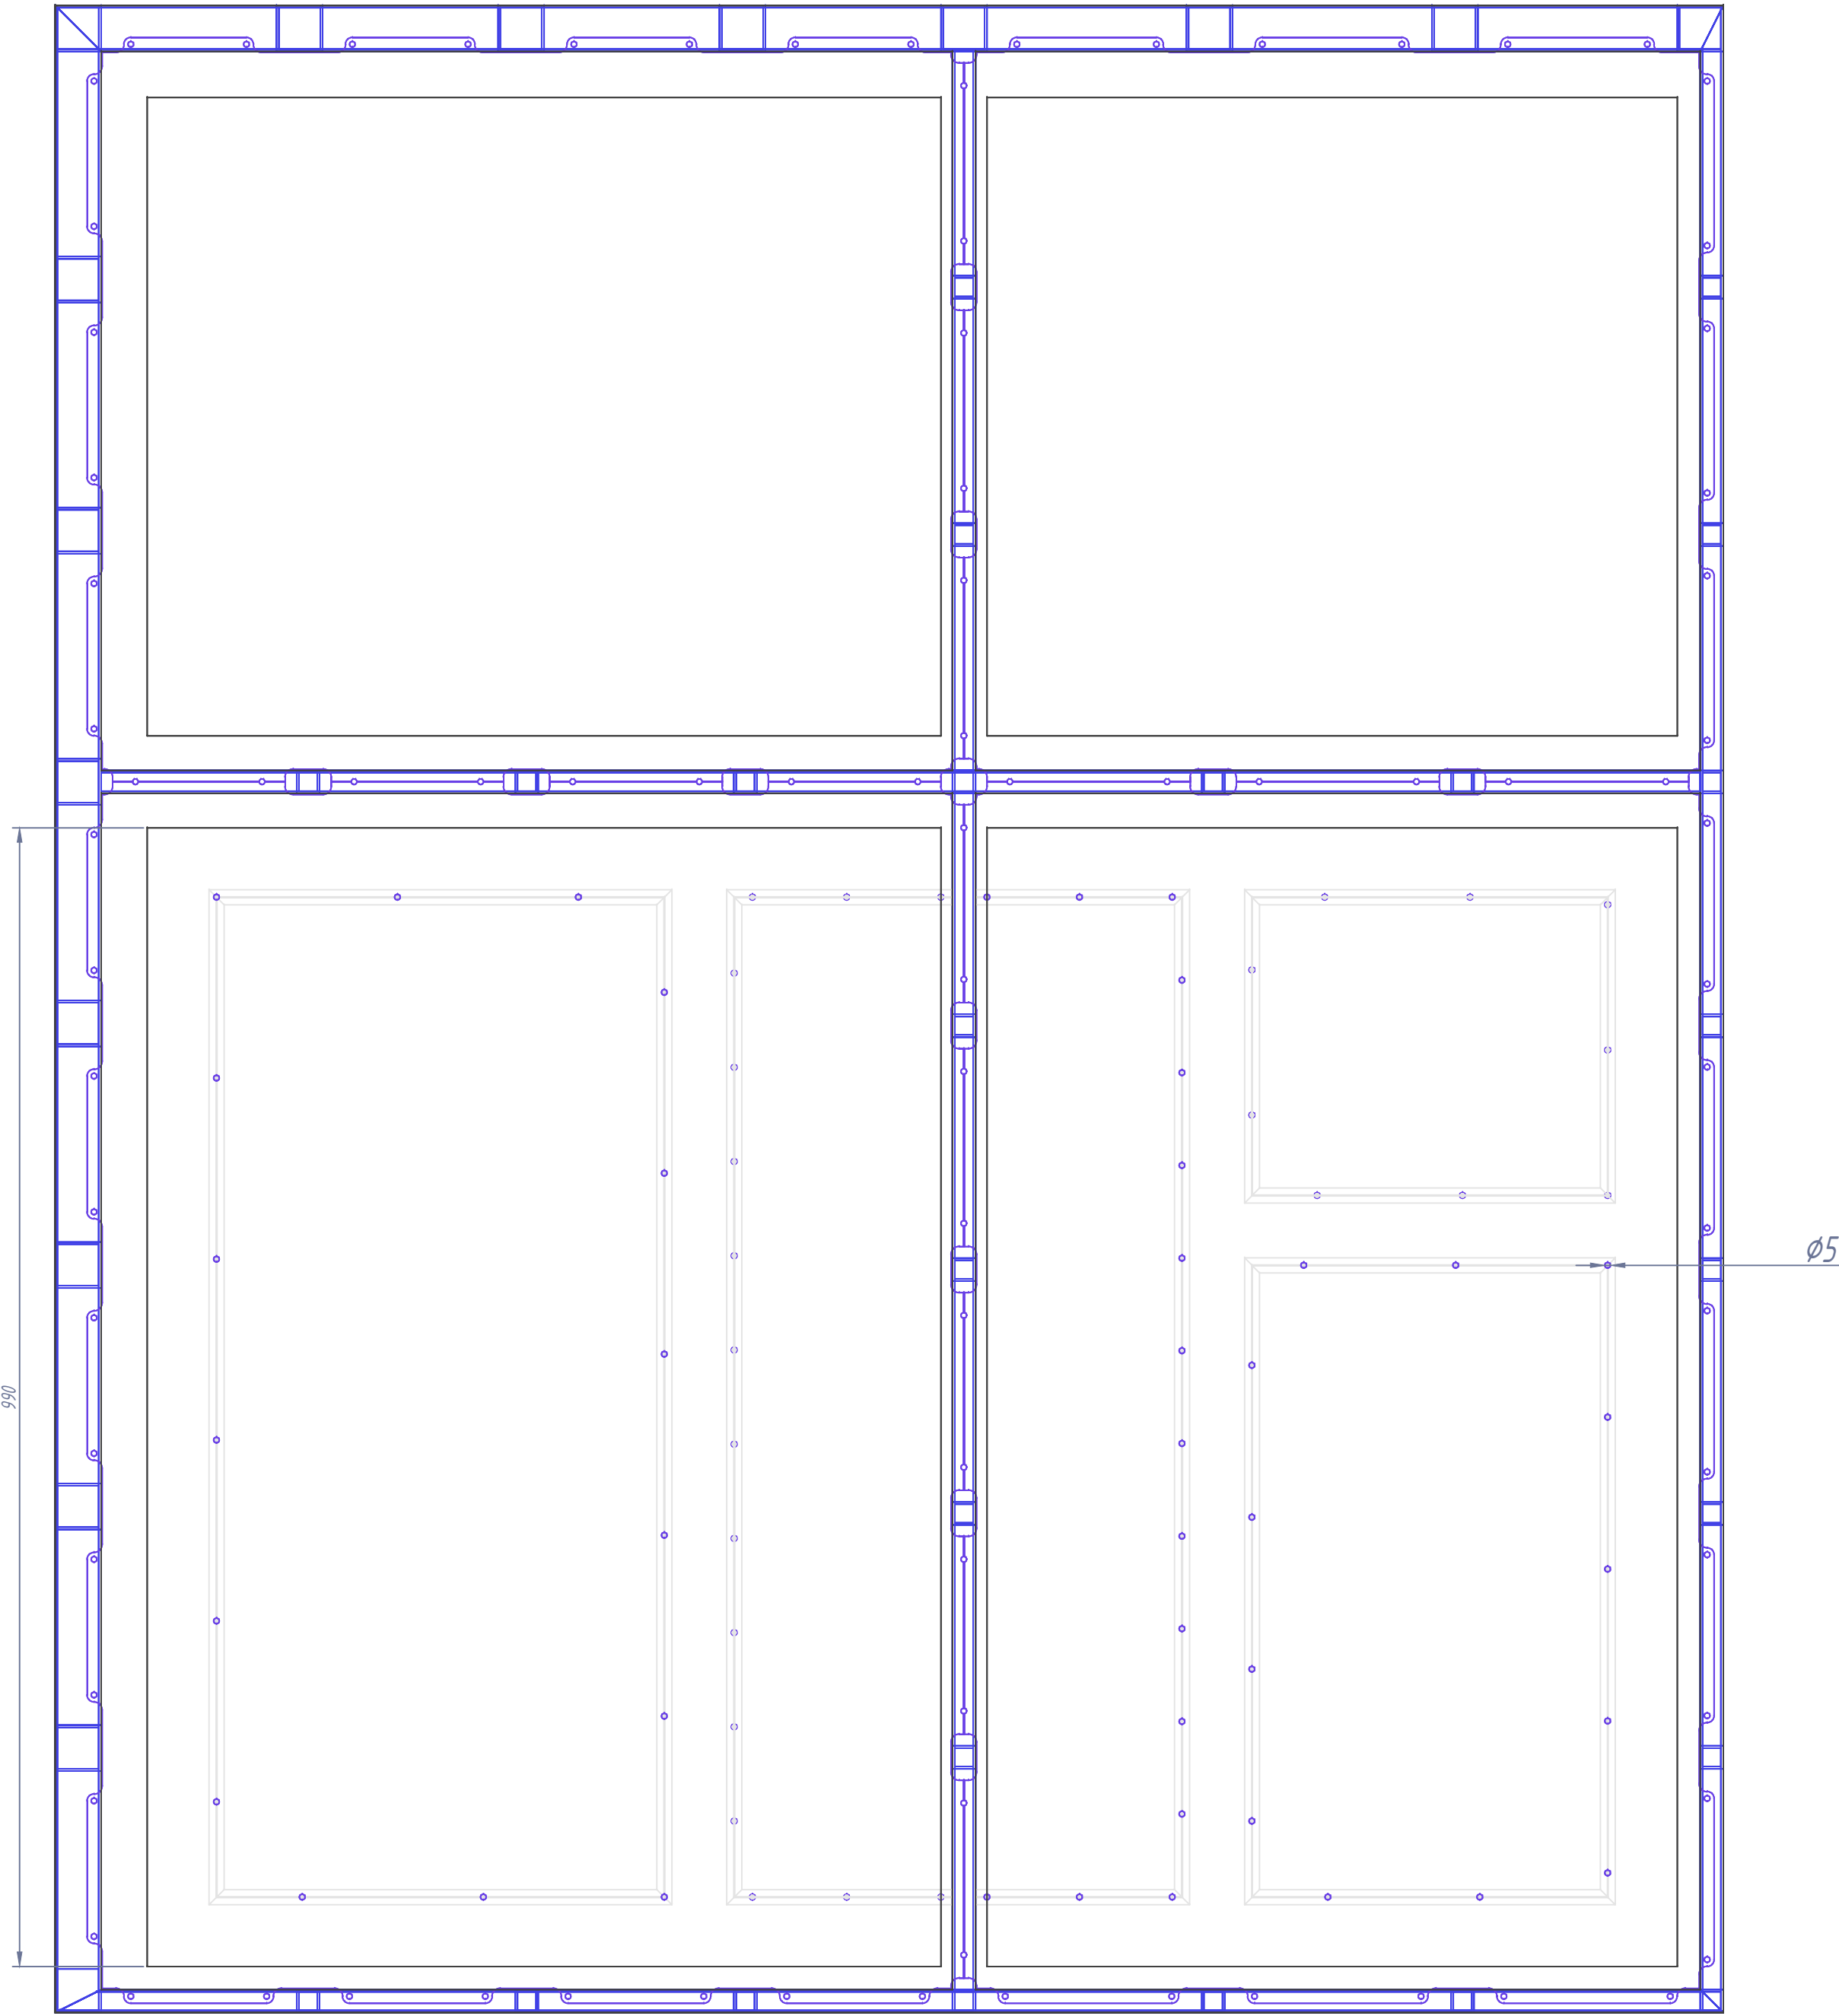

1. Выполнить каркас из алюминиевого профильного проката сечением 40 х 20 х 1,5 мм .
2. Выполнить обшивку каркаса с лицевой стороны окрашенной (RAL 9007) фанерой по контуру конструкции ,в 2 этапа - фанера 6 мм- транслюцентный банер – фанера 6 мм.
3. Выполнить обшивку каркаса с тыльной стороны алюминиевой пластиной 1мм.
4. Выполнить перетяжку лицевой стороны транслюцентным банерным материалом см. п 2.
5. Выполнить все соединения сварным способом.
6. Предусмотреть крепление фанеры к лицевой части каркаса саморезами с равномерным шагом, обеспечивающим надежную фиксацию и отсутствие деформаций .
7. Предусмотреть удаление всех заусенцев и острых кромок на металлических деталях после сварки .
8. Выполнить контроль геометрических размеров и соответствия конструкции чертежу с допусками не более 1мм .
9. Предусмотреть качество поверхности металла без дефектов , трещин , вмятин и коррозии .
10. Выполнить защитное покрытие металлоконструкции согласно техническим требованиям (при необходимости).
11. Предусмотреть маркировку и упаковку изделия для сохранности при транспортировке и хранении .

ТХОС 1.02.-00				“Молодожены” Богомалов К.			
Проверил	Фамилия	Подпись	Дата	Фронтальная стена . Лайтдокс 1-1.1 Конструктив		Литера	Масса
	Галич В.В.					у	Размеры
Принял	Галич В.В.			ГБУК г.Москвы “Театр на Малой Бронной”		Лист	Листов
Чертил	Глухов И.А.						
						Школа -студия МХАТ	